

广东省村庄规划编制指引

(试行)

广东省住房和城乡建设厅
二〇一八年八月

目 录

第一章 总则	1
1.1 编制目的	1
1.2 适用范围	1
1.3 基本原则	2
1.4 规划依据	3
1.5 规划期限	3
1.6 规划范围	3
第二章 现状调查	4
2.1 社会经济情况	4
2.2 自然环境情况	4
2.3 历史文化情况	4
2.4 土地利用情况	4
2.5 规划政策情况	5
2.6 村庄建设需求	5
第三章 规划内容	5
3.1 产业生态	5
3.2 用地布局	6
3.3 公共服务设施和公用工程设施	7
3.4 历史文化保护	8
3.5 村庄安全和防灾减灾	9
3.6 特色风貌和农房整治	9
3.7 实施保障	10
第四章 规划成果	10
附表1: 村庄建设需求台账	i
附表2: 村庄规划/近期建设项目库(表)	ii
附表3: 村庄用地规划汇总表	iii
附表4: 村民公众参与报告书	iii
附件 广东省社会主义新农村示范村整治创建规划优秀案例参考	i

第一章 总则

1.1 编制目的

为全面贯彻党的十九大精神，深入实施乡村振兴战略，落实《中共中央 国务院关于实施乡村振兴战略的意见》和《中共广东省委 广东省人民政府关于推进乡村振兴战略的实施意见》（粤发〔2018〕16号）工作部署，根据省委办公厅、省府办公厅《关于全域推进农村人居环境整治建设生态宜居美丽乡村的实施方案》（粤办发〔2018〕21号）有关要求，规范我省村庄规划编制，引导生态宜居美丽乡村建设，依据相关法律法规和技术规范，结合我省实际，制定本指引。

1.2 适用范围

本指引适用于本省农村地区及城镇规划区内未纳入城镇规划管辖的行政村，开展“多规合一”的村庄规划编制和管理实施。

连片建设发展的多个行政村，可按区域统筹思路合并编制村庄规划。已编制规划的村庄，应依据本指引整合规划成果并进一步修编完善。有条件的自然村（20户以上，下同）可参考本指引单独编制村庄规划。

在符合本指引的基础上，各县（市、区）可根据实际情况明确有关细则。已编制整治创建规划的省定贫困村，无需重复编制规划。

1.3 基本原则

(1) 规划先行，注重实施

突出规划的引领作用，以目标为导向制定切实可行的行动计划，建立建设项目库，按照先规划后建设、不规划不实施的工作模式，提高规划的科学性和可操作性，强化村庄规划的法定地位。

(2) 因地制宜，彰显特色

充分考虑村庄生态环境、资源条件、建设基础、社会经济发展水平等各项因素，编制因地制宜、切合实际的村庄规划。尊重地方民俗风情和村民生活习惯，强化乡村特色资源的保护、传承和活化利用，彰显广东地域文化特色。

(3) 尊重民意，多方协作

充分尊重村民意愿，激发村民参与村庄规划编制和实施的积极性和主观能动性，建立村民、政府、企业、规划师多方协作联动的规划编制工作机制，打造共建共享共治的村庄治理模式。

(4) 多规融合，生态宜居

做好规划衔接、促进“多规合一”，保障生产空间集约高效、生活空间宜居适度、生态空间山清水秀。以建设生态宜居美丽乡村为导向，加强生态治理和保护，优化提升乡村建设质量，培育发展绿色生态新产业、新业态。

(5) 简明规范，通俗易懂

规划成果应简明扼要、规范严谨、通俗易懂，做到村民易懂、村委能用、政府好管。

1.4 规划依据

《中华人民共和国城乡规划法》、《广东省城乡规划条例》、《村庄规划用地分类指南》、《村庄整治技术规范》、《土地利用现状分类》等法律法规和技术标准、规范；县（市）域乡村建设规划、镇（乡）总体规划和土地利用总体规划等上位规划及专项规划。

1.5 规划期限

村庄规划期限原则上为 5-10 年，并应与县（市）域乡村建设规划、镇（乡）总体规划等上位规划的规划期限相衔接。其中，近期规划期限为 3-5 年。

规划期满后，如村庄用地规划、设施规划等核心内容与上位规划的强制性内容无重大冲突的，经村民大会或村民代表大会同意并报县级人民政府审核通过，可将该村庄规划的规划期限适当延长。

1.6 规划范围

村庄规划范围为本村行政区域。自然村编制村庄规划可根据实际需要划定规划范围。

第二章 现状调查

通过走访座谈、现场踏勘、问卷调查和驻村体验等方式开展实地调研，全面了解村庄基本情况、现状特征、主要问题、发展诉求等，明确规划目标和规划重点，建立村庄建设需求台账。

2.1 社会经济情况

包括户数、户籍人口、人口迁入迁出、人均纯收入、集体收入、主导产业、社会治理状况等，发展旅游的村庄应增加旅游人次、周期、收入等有关调查内容。

2.2 自然环境情况

包括地形地貌、工程地质、水文、气象、自然资源（土地、水、矿产、生物）、生态环境（基本农田保护区、山地、水体、园林）等。

2.3 历史文化情况

包括历史文化名村、传统村落、文物保护单位等历史建筑或传统风貌建筑，风水塘、牌坊、古井、古树名木等历史环境要素，古驿道、古驿站等历史遗存，口头传统、宗祠祭祀、民俗活动、礼仪节庆、传统表演艺术和手工技艺等非物质文化遗产要素。

2.4 土地利用情况

包括土地利用、用地权属、农房建设及权属、交通水利、公共服务设施、公用工程设施、环境绿化美化建设等。

2.5 规划政策情况

包括国民经济和社会发展规划、各类城乡规划¹、土地利用总体规划等上位规划及相关规划，镇（乡）、村庄发展的相关政策和管理制度，以及规划所需工作底图（比例尺不低于 1:2000 的地形图或高分航摄正射影像图）。

2.6 村庄建设需求

根据村庄现状摸查和村民发展诉求分析，结合县（市）域乡村建设规划的相关要求，确定村庄建设需求和规划重点，建立村庄建设需求台账（参见附表 1）。

第三章 规划内容

结合现状调查和村庄建设需求台账，以建设生态宜居美丽乡村为目标，围绕本章各项规划内容，开展针对性的村庄规划编制，并形成村庄规划建设项目库（表）（参见附表 2）。各地区根据村庄发展阶段、发展条件和改善农村人居环境的总体工作部署，可在地方管理细则或县（市）域乡村建设规划中，进一步明确有关规划内容的编制深度。

3.1 产业生态

¹ 包括但不限于城市（县）总体规划、镇（乡）总体规划等法定规划以及县（市）域乡村建设规划、综合交通、历史文化保护等专项规划。

结合地区发展条件、发展要求，统筹村庄产业发展体系，引导打造“一村一品”。根据改善农村人居环境的总体思路，统筹制定村庄生态环境保护措施。主要内容应包括：

（1）明确村庄产业定位，提出产业发展思路和策略；

（2）统筹安排一二三产的功能布局，确定农林牧渔生产区、农副产品加工区、旅游发展区等产业集中区的范围和规模；

（3）落实村庄生态环境保护、畜禽养殖废弃物处理或资源化利用等措施。

3.2 用地布局

综合现状调查、上位规划、地籍调查和土地确权等资料，结合村庄自然生态环境、产业分布和居民点聚落特征，确定村庄规划区范围和用地布局。主要内容应包括：

（1）明确生态保护、产业发展、村庄建设的主要区域，划定村庄规划区范围，有条件的应按照“多规合一”的要求落实各类控制线（如永久基本农田保护控制线、生态控制线）；

（2）进行人口预测，确定村庄各类建设用地的分布、规模和范围线，制定村庄用地规划汇总表（参见附表3）。村庄建设用地规模和范围线应符合城市（镇）总体规划“三区四线”管控要求，并与土地利用总体规划相衔接；

（3）明确村庄各类新建、改建、扩建项目的用地位置、

规模和范围线，作为核发乡村建设规划许可证的依据；

（4）对因土规规模核减、整村搬迁等产生村庄用地变更的情况，应编制有关范围的用地控制方案，提出近期村民自建房管理的措施。

3.3 公共服务设施和公用工程设施

公共服务设施规划应结合村民生产生活圈，分类分级配套完善村庄公共服务设施。优先保障托幼、养老、医疗、文化康体等宜居生活配套，鼓励新建与改建相结合。主要内容应包括：

（1）确定各类设施的数量和选址位置；

（2）明确各类设施的建设规模（独立占地的应包括用地面积和建筑面积），划定范围线；

公用工程设施规划应结合居民点分布和现状建设条件，优先解决村庄道路硬化、生活垃圾和污水处理、卫生改厕等人居环境整治重点问题，各类设施布置应兼顾村民使用方便和管理维护的需要，鼓励有条件的连线连片村庄设施共建共享。主要内容应包括：

（1）衔接上位规划和相关专项规划确定的区域干线和城市干道，确定村庄对外道路系统优化方案；

（2）提出村道拓宽、改造提级方案，确定需硬化村道的线路和硬化模式，提出具体的硬化要求和改造措施；

（3）结合村民生活和产业发展需要，统筹安排公共停

车场的分布和数量；

（4）确定村庄生活垃圾收运处理方式，合理配置生活垃圾收集点、垃圾箱、清运工具，提出村庄保洁方案；

（5）确定污水处理模式，制定雨污分流措施和污水管道改造升级方案；

（6）结合乡村旅游等特色产业发展和村民生活需要，提出标准化公厕配建方案；

（7）明确供水、电力、供气、电信等设施的位置、规模、线路敷设等建设要求。

3.4 历史文化保护

结合村庄现状各类历史要素调查，尊重传统村规民俗，兼顾历史文化的保护与活化利用，制定相关措施。主要内容应包括：

（1）提出村庄历史文化保护原则，确定保护对象，划定保护范围，建立保护名录，明确相应保护要求；

（2）对历史文化名村、传统村落、文物保护单位、历史建筑、传统风貌建筑、古树名木等物质文化遗产，以及口头传统、宗祠祭祀、民俗活动、礼仪节庆、传统表演艺术和手工技艺等非物质遗产提出保护传承与活化利用的措施；

（3）对拥有古驿道资源的村庄，在做好普查、保护及修复工作基础上，建立古驿道标识系统等配套服务设施，提出整合串联沿线历史文化遗产、生态、旅游等资源的策略。

3.5 村庄安全和防灾减灾

综合考虑各类灾害的影响，建立村庄综合防灾体系。主要内容应包括：

（1）制定防洪防涝、地质灾害防治、消防等村庄安全和防灾减灾措施；

（2）与地方政府的应急预案相协调，提出村庄应急庇护场所选址及建设要求；

（3）提出农村建房安全管理要求，避免因违规削坡建房诱发次生危害。

3.6 特色风貌和农房整治

挖掘和提炼村庄自然、人文要素符号及岭南传统乡土建筑特色，兼顾村民实用和现代审美的需要，提出村庄特色风貌打造和旧村农房整治的措施。主要内容应包括：

（1）明确旧村整治范围和新建、改建、拆除的房屋边界，提出危旧房改造要求；

（2）对重要公共区域周边的房屋外立面提出美化或修缮的措施；

（3）因地制宜提出村民自建房设计意向，明确建筑风格、色彩、选材等方面的设计要求；

（4）对晒场、戏台等村庄传统空间和活动广场、运动场所等开敞空间，以及“三清三拆”整理出来的空闲地、插花地、夹心地，提出改造利用方案；

(5) 提出利用乡土树种和本土农产进行清旧补绿、拆旧建绿的措施，制定街巷、房前屋后等绿化美化指引，有条件的可对重要节点制定景观绿化设计方案。

3.7 实施保障

结合地方政府发展部署和村庄管理的实际，统筹安排村庄分期实施计划，制定近期行动方案，并提出相关保障措施。

第四章 规划成果

村庄规划成果应包括“4图2书2表1公约”：

“4图”，指4张主要图纸，分别是：

村庄用地现状图，标示现状各类用地分布、道路、公共服务设施和公用工程设施布点，并附村庄用地现状汇总表和现状设施一览表；

村庄用地规划图，标示村庄规划用地布局、道路、公共服务设施和公用工程设施布局，并附村庄用地规划汇总表（参见附表3）和规划设施一览表；有需要的可增加有关规划控制线，如村庄建设用地范围线、新村建设范围线、旧村整治范围线、紫线等；

村庄建设项目布局规划图，标示村庄道路、设施、绿化景观等建设项目布局，并附村庄规划建设项目库（表）；

农房建设总平面图，选取1个示范（自然）村进行绘制，标示新建、改建、修缮等各类农房的位置、范围，提出设计

意向或效果图。

上述图纸应采用比例尺为 1:1000-1:2000 的地形图作为底图，条件不具备或确有必要的，也可采用高分航摄正射影像图作为底图，但应增加标示必要的定位信息。

“2 书”指规划说明书和公众参与报告书（参见附表 4）。

“2 表”指 2 套表格，分别是村庄建设需求台账和村庄规划建设项目库（表）。

“1 公约”指村庄规划建设管理公约。参照传统村规民约，内容应包括规划核心要求，如村庄建设用地安排、房屋报建、设施维护、历史文化保护等，并应做到“行文易懂、内容好记、管理可行”。

其它规划内容可根据需要增加有关规划图纸。

有条件的村庄，应增加各自然村近期建设项目布局规划图，并附近期建设项目库（表）。

附表 1：村庄建设需求台账

序号	类型	设施名称	数量	是否独立用地	用地面积 (m ²)	建筑面积 (m ²)	所在位置	服务对象	覆盖程度 (户)	备注
1	基础设施配套	道路交通		①是； ②否；				服务本村		
2		供水设施								
3		供电设施								
...		燃气设施								
		路灯设施								
		村道硬化	长度：-----米							
		防震减灾场所								
		...								
	环境卫生	垃圾收集点								
		污水处理设施								
		...								
	公共服务设施	公共服务中心								
		网络工程								
		通信工程								
		卫生站								
		教育设施								
		文体设施								
		养老设施								
		...								
	村庄建设管理	农房建设								
		...								
	历史文化保护	传统村落								
		南粤古驿道								
		...								
	绿化风貌	村庄绿化								
		村道绿化								
		乡村公园								
		...								
	产业发展	× × 产业设施								
		...								

注：表内“设施名称”可根据调研实际情况增加。

附表 2：村庄规划/近期建设项目库（表）

序号	项目类型	近期建设项目分类	项目名称	空间位置	用地面积 (m ²)	建筑面积 (m ²)	投资规模估算 (万元)	资金筹措	资金计划到位时间	主管部门	协作部门	建设时序	备注
1	垃圾处理	有机易腐垃圾处理设施											
2		垃圾收集点											
3													
...	污水处理	污水处理设施建设											
		污水管网建设											
													
	农房整治	危房改造任务											
													
	村道硬化	农村公路建设											
		村内巷道硬化											
													
	设施完善	公共服务中心(站)											
		卫生站											
													
	历史文化保护	南粤古驿道保护利用											
													
	产业发展	休闲观光农场											
		民宿											
													
	绿化美化	乡村公园											
		庭院绿化											
													
													

注：（1）建设时序：需填写建设项目的起止时间（__年__月至__年__月），对于未能确定开工建设时间的项目，应预测项目建设周期。

附表 3：村庄用地规划汇总表

用地 代码	用地名称		用地面积 (hm ²)		占总用地面积 的比例 (%)		人均村庄建设用 地面积 (m ² /人)	
			现状	规划	现状	规划	现状	规划
V	村庄建设用地							
	其中	V1 居住用地						
		V2 村庄公共服务用地						
		V3 村庄产业用地						
		V4 村庄基础设施用地						
		V9 村庄其他建设用地						
N	非村庄建设用地						—	—
	其中	N1 对外交通设施用地					—	—
		N2 国有建设用地					—	—
E	非建设用地						—	—
	其中	E1 水域					—	—
		E2 农林用地					—	—
		E9 其他非建设用地					—	—
总用地范围					100	100	—	—
备注： _____年现状常住人口_____人（其中： 户籍人口_____人） _____年规划常住人口_____人								

附表 4：村民公众参与报告书

村民参与报告书可包括但不限于以下部分：

（一）规划前期意见征询

表达意见征询的方式、时间、地点、对象、内容等，记录村民规划诉求。

（二）规划初步方案意见征询

表达意见征询的方式、时间、地点、对象、内容等，记录村民意见和落实情况。

（三）村民大会或者村民代表大会审议

表达村民大会或者村民代表大会审议的时间、地点、村民出席情况、村民表决情况等，记录村民意见和落实情况。


（四）规划方案批前公示

表达规划方案批前公示的时间、地点、内容等，记录村民意见和落实情况。


附件 广东省社会主义新农村示范村整治创建规划优秀案例参考

(一) 韶关市翁源县翁城镇明星村社会主义新农村示范村整治创建规划


1.村庄现状情况图

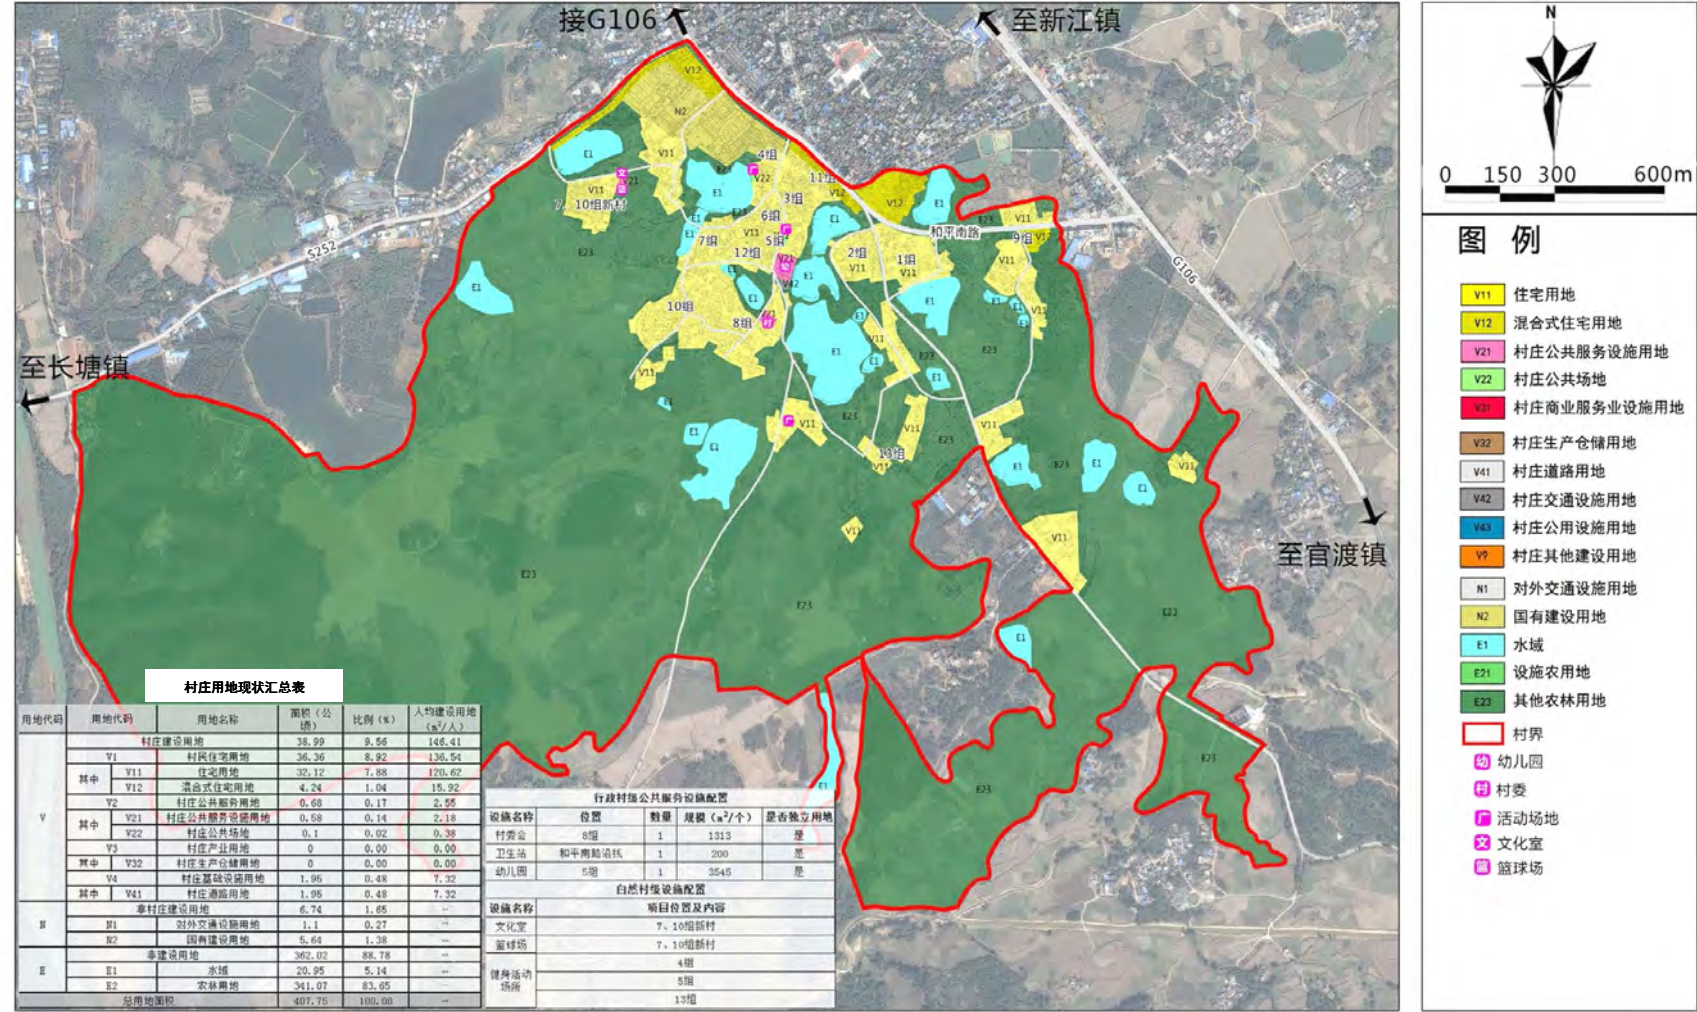

2.村庄用地布局规划图

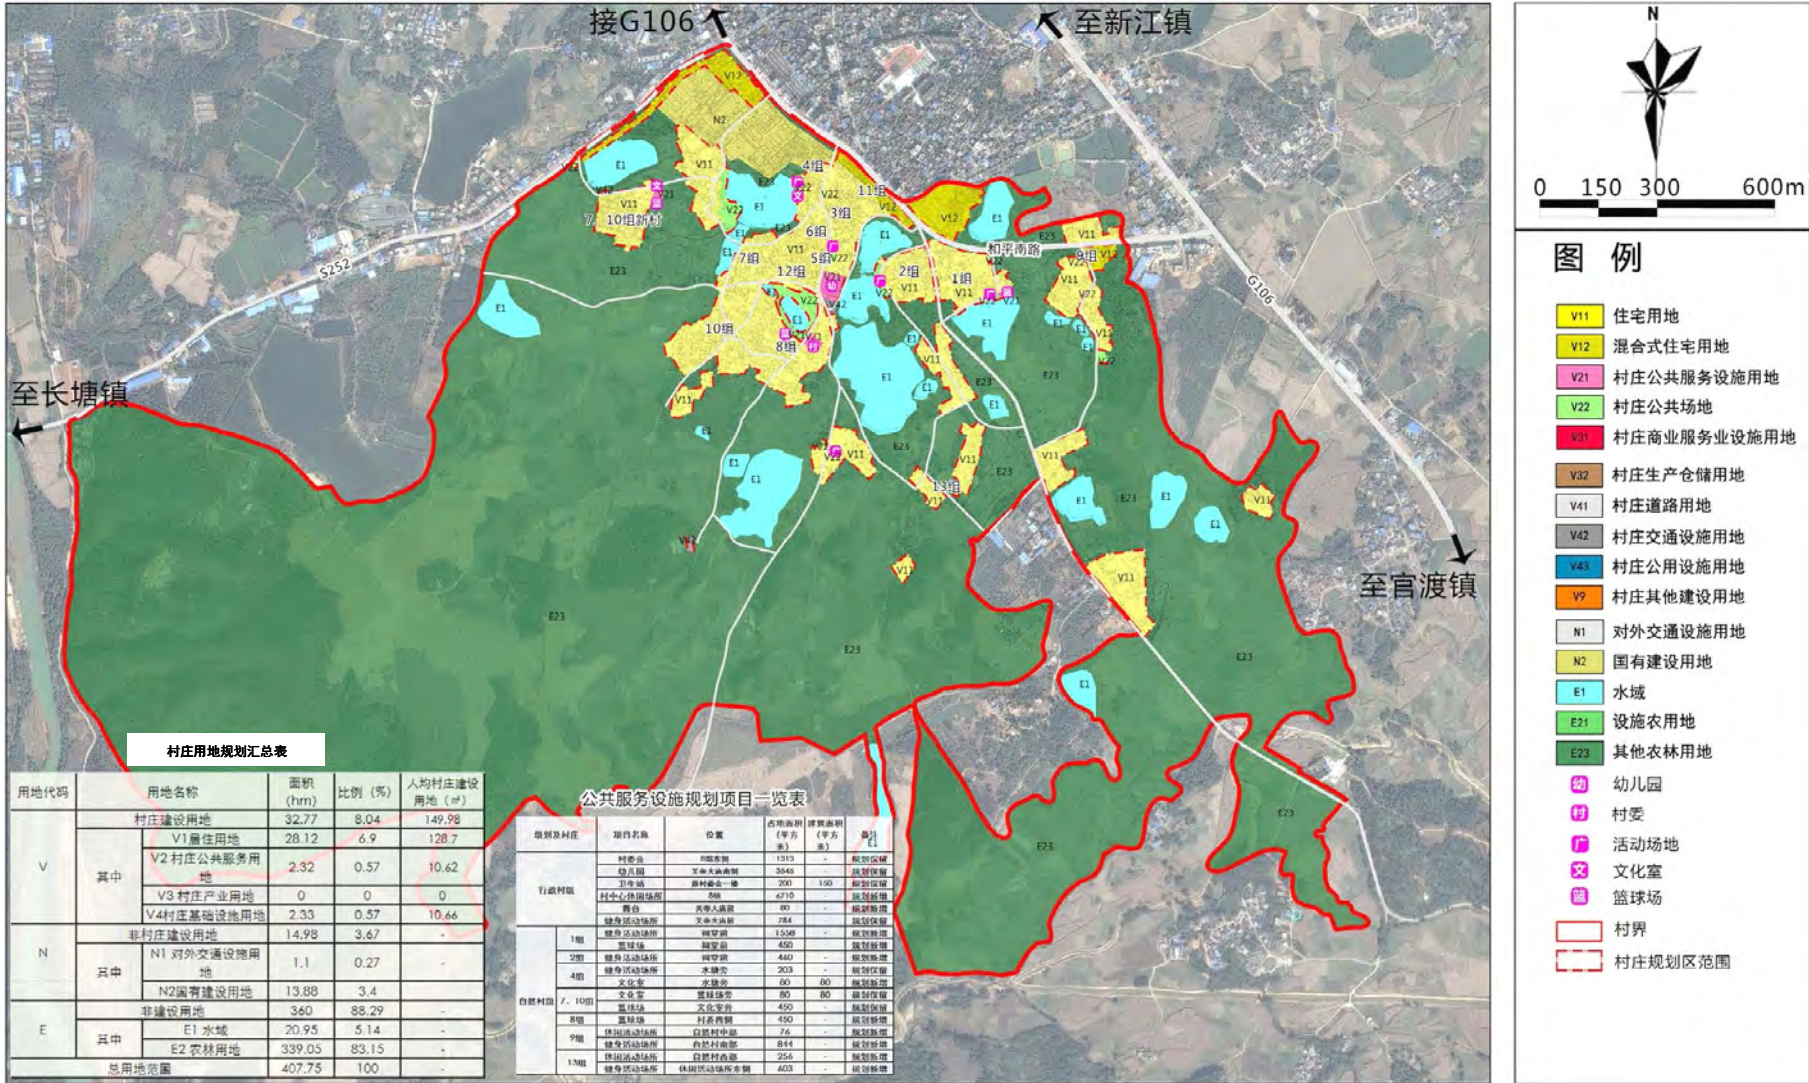

3.村庄规划建设项目布局图

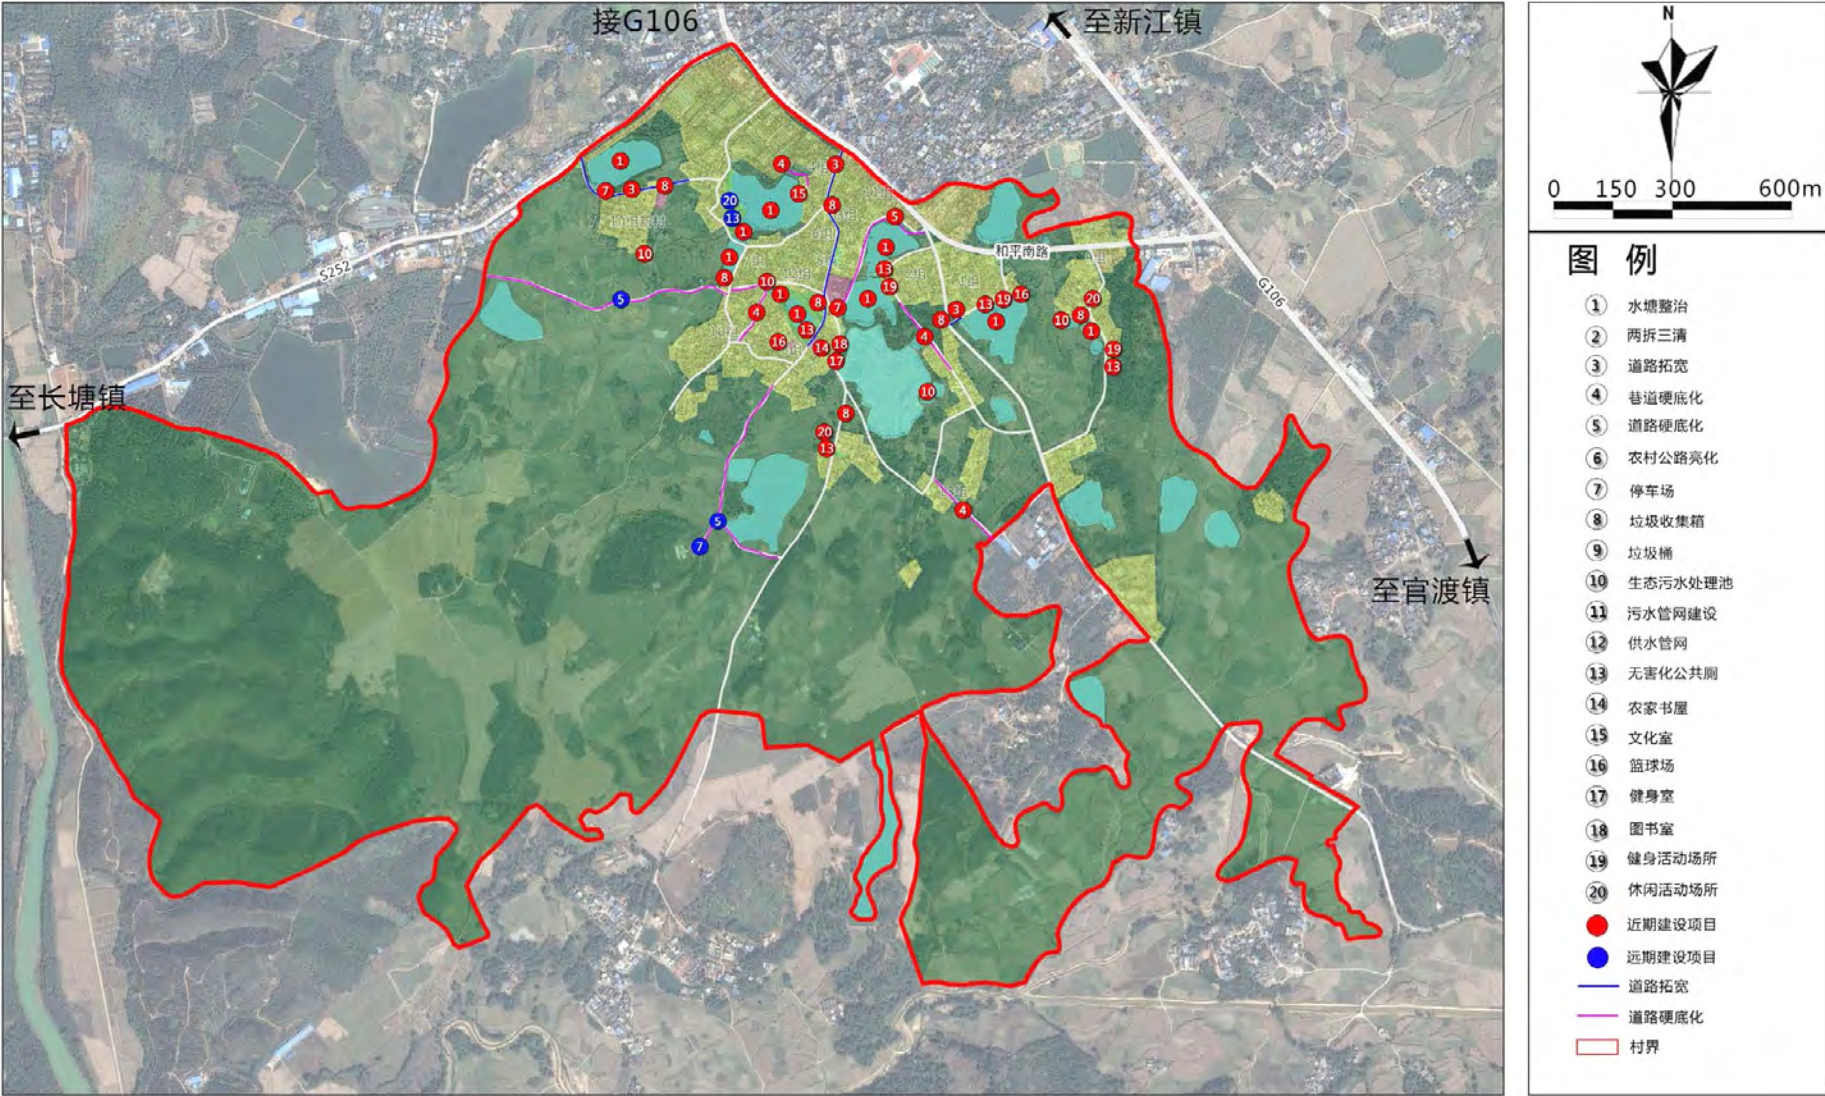

4. 农房建设规划平面图

分类整改，清拆、整治、保留并举，重塑村庄传统格局，提升建筑风貌。
规划范围内现状建筑391栋，规划清拆建筑6栋，修缮建筑3栋，
整治建筑14栋，新建建筑1栋，保留建筑367栋。



修缮建筑：

修缮上何老围屋，包括立面整治、结构加固、屋顶修复、周边环境美化等。



清拆建筑：

主要清拆村内已经破损较为严重的泥砖房和违建铁棚。



整治建筑：

重点对沿社道的民居和沿主要巷道的传统民居建筑进行立面整饰。风格统一，针对裸露墙体进行粉刷和景观美

新建建筑：

规划结合村民建设诉求，由村民自筹新建农房建筑。





改造前

墙体白色外
墙涂料刷新

修缮楼梯、
栏杆等构
件

收拾杂物，直
接运用农具作
为装饰

更换破损瓦面

修缮破损门窗构件

墙台添加蔬花果盆栽

改造后



5.村庄建设需求台账

序号	类型	设施名称	数量	是否独立用地	用地面积 (㎡)	建筑面积 (㎡)	所在位置	服务对象	覆盖程度 (户)	备注
1	村容村貌	沿街新建筑立面整饰	80 栋	是	-	-	和平南路沿线	本村	沿路住户	-
2		老旧建筑外立面修缮	18 栋	是	-	-	9 组	本组	20 户	-
3		旧牌坊周边环境整治提升	-	否	-	-	旧牌坊处	本村	全部	对旧牌坊及周边环境进行整治
4		路口标识	-	否	-	-	新建道路入口处	本村	全部	按照村委会门口风格，新建标识
5		7、10 组组名石	-	否	-	-	7、10 组村口	本组	48 户	-
6		1 组组名石	-	否	-	-	1 组村口	本组	49 户	-
7		9 组组名石	-	否	-	-	9 组村口	本组	50 户	-
8		乱搭乱建拆除	-	-	-	-	全村	本村	全部	-
9		空置宅基地清理	-	是	-	-	全村	本村	全部	-
10		宅前空地整治	-	是	-	-	全村	本村	全部	-
11		水塘整治	-	是	-	-	全村	本村	全部	对水塘进行清淤，并设置护栏，提升周边景观风貌
12	基础设施	村道升级	旧牌坊到村委会道路 658 米	是	-	-	全村	本村	全部	对有条件的路段进行拓宽或增加会车场
13			拓宽 338 米道路	是	-	-	7 组、10 组	本村	全部	规划往北拓宽道路至 7 米宽（现有道路宽 4 米）
14		村道硬化	环村道路已硬化 5.8 公里，需硬化 1.8 公里，村内道路目前硬化了约 75%，还需 25%	是	-	-	全村	多组	全部	-
15		停车场	4 个	是	-	-	7 组、10 组、	多组	525 户	生态停车场
16		人行道	563m	是	-	-	7 组、8 组、9 组、10 组	多组	全部	-
17		绿化	1.06 公顷	是	-	-	7 组、8 组、9 组、10 组	多村	全部	-
18		路灯设施	主要村道 50 个高路灯，村内道路 130 矮路灯穿插在村内	否	-	-	主村路、次村路	本村	全部	-
19		防震减灾场所	目前以幼儿园关帝庙前广场和篮球场等为避难场所，无需新设	否	-	-	富陂小学、广场	多组	全部	-

序号	类型	设施名称	数量	是否独立用地	用地面积 (㎡)	建筑面积 (㎡)	所在位置	服务对象	覆盖程度 (户)	备注
20	基础设施	垃圾收集箱	18个	否	-	-	全村	本村	全部	结合各自然村大型节点设置，外观材料建议采用竹材、木材等材料。
21		污水处理设施	目前无，需要3个	是	-	-	7和10组新村、9组、8组	本村	全部	面积由计算确定
22		公厕	4个	是	-	-	7组、8组、1组、9组	多村	全部	结合休闲场所设置
23	公共服务设施	公共服务中心	已有一个在建，无需新设	是	1313	800	8组旁	本村	全部	-
24		网络工程	已接入网络，无需新设	是	-	-		本村	全部	-
25		通信工程	已接入网络，无需新设	是	-	-		本村	全部	-
26		卫生站	已有1个，无需新设	是	-	-	和平南路沿线	本村	全部	-
27		教育设施	现有1个幼儿园，无需新设	是	10760	>7000	幼儿园	多村	全部	-
28		文体设施	2个篮球场，4处健身场所	是	-	-	8组、1组、2组、9组、13组	本村	全部	1、2、9、13组新增健身场所，1、8组新增篮球场
29		文化活动中心	4组需要新增1个文化活动中心	是	80	80	4组	本组	全部	-
30		养老设施	目前结合村委会，规划可结合文化室打造	否	-	-	村委会、4组	本村	全部	-
31		快递服务点	-	否	-	-	和平南路沿线	多村	全部	-
32		戏台	1个	是	80	-	关帝庙前广场	本村	全部	-
33	村庄建设管理	理事会中心	结合村委会	否	-	-	村委会	本村	全部	-
34	村庄绿化	道路绿化提升	658米	是	-	-	旧牌坊到村委会路段	本村	全部	提升道路两侧景观，增加绿化
35	美化	墙绘	-	否	-	-	各村小组	本村	全部	利用砖瓦房、祠堂墙体等绘制体现村庄精神文明的墙绘
36	产业发展	农民公寓	3栋	是	-	-	旧牌坊旁	本村	全部	利用旧村委会建设3栋6层的公寓，租金作为村财政收入

6.村庄规划建设项目库（表）

序号	项目类型	整治项目分类	项目名称	空间位置	建设规模	投资规模估算 (万元)	资金筹措	资金计划 到位时间	主管部门	协作部门	整治时序	备注
1	村容村貌整治	水系景观提升	水塘整治	村域	24218m ²	726	省定贫困村资金	2018 年	政府部 门	明星村 村委	2018-2019 年	清理水塘淤泥、垃圾，池壁维持原貌生态驳岸； 增加绿化等。
			栏杆	村域	1451m	50.8	省定贫困村资金	2018 年			2018-2019 年	花岗岩栏杆
2	两拆三清	两拆三清	村域	——	——	村民自筹	2018 年	2018-2019 年			拆除残垣断壁、拆违搭建；清理村巷道乱 堆乱放、乱拉线；清理房前屋后杂草杂物、 卫生死角；清理沟渠池塘小溪河淤泥、垃圾。	
3	基础设施完善 行动	道路交 通	道路拓宽	7、10 组新 村道路	342m	17.5	省定贫困村资金	2018 年			2018-2019 年	现状水泥路宽 4.5 米，规划拓宽 1 米车行道，1.2 米人行道，铺设水泥并画人行道标识
4			巷道硬底化	8 组、13 组	533m	36.8	省定贫困村资金	2018 年			2018-2019 年	对村内未硬底化的巷道进行硬底化，宽 3m， 可采用水泥等材料。
5			村道硬底化	2 组、7 组	846m	68.1	省定贫困村资金	2018 年			2018-2019 年	对村内未硬底化的村道进行硬底化，宽 3.5m， 可采用水泥等材料。
				2 组至幼儿 园	409m	32.9	省定贫困村资金	2018 年			2018-2019 年	对村内未硬底化的村道进行硬底化，宽 3.5m， 可采用水泥等材料。沿水塘一侧 采用毛石堆砌。
				至烈士陵园 路段	670m	54	市县配套资金	2018 年			2018-2019 年	对村内未硬底化的村道进行硬底化，宽 3.5m， 可采用水泥等材料。
6			农村公路亮 化	村道	35 盏	17.5	省定贫困村资金	2018 年			2018-2019 年	高路灯，按间隔 40 米、单侧设置路灯
				巷道	59 盏	20.7	省定贫困村资金	2018 年			2018-2019 年	矮路，灯穿插在村内
7			停车场	烈士陵园	607 m ²	18.2	市县配套资金	2018 年			2018-2019 年	设置植草铺砖生态停车位
				幼儿园门前	584 m ²	13.4	村民自筹	2018 年			2018-2019 年	混泥土
				7、10 组新 村	260 m ²	7.8	省定贫困村资金	2018 年			2018-2019 年	设置植草铺砖生态停车位
8	垃圾处 理	垃圾收集箱	村域	7 个	7	省定贫困村资金	2018 年	2018-2019 年			结合各自然村主要村道设置。	
垃圾桶		村域	45 个	3.6	省定贫困村资金	2018 年	2018-2019 年	生活垃圾收集桶				


序号	项目类型	整治项目分类	项目名称	空间位置	建设规模	投资规模估算 (万元)	资金筹措	资金计划 到位时间	主管部门	协作部门	整治时序	备注
10	基础设施完善行动	污水处理	生态污水处理池	7、10 组新村	1 个	40	省定贫困村资金	2018 年			2018-2019 年	100% 生活污水处理，采用无动力“分散式微型人工湿地+生态沟”生态处理系统技术；整体项目具体实施及建设由县层面统筹。
				8 组、9 组、13 组	3 个	120	PPP 项目	2018 年			2018-2019 年	100% 生活污水处理，采用无动力“分散式微型人工湿地+生态沟”生态处理系统技术；整体项目具体实施及建设由县层面统筹。
11			污水管网建设	7、10 组新村	0.9km	36	省定贫困村资金	2018 年			2018-2019 年	采用 PVC 管收集每家每户的生活污水，入户管径为 DN110，主管为 DN200-400。
				村域	7.0km	——	PPP 项目	2018 年			2018-2019 年	采用 PVC 管收集每家每户的生活污水，入户管径为 DN110，主管为 DN200-400。
12		集中供水	供水管网	村域	9.3km	——	市县配套资金	2018 年			2018-2019 年	给水支管沿入村道路进行敷设，管径为 100mm，其中接入自然村管线为 7.1km。
13		公共厕所	无害化公共厕所	1 组、2 组、7 组、8 组、9 组、13 组	16 ㎡ / 处	25.8	省定贫困村资金	2018 年			2018-2019 年	结合休闲场所设置
14	公共服务设施完善行动	公共设施	农家书屋	结合村委设置	10 ㎡	5	省定贫困村资金	2018 年	2018-2019 年	结合村委设置，完善农家书屋的书籍、电脑等设施，为村民提供借阅、上网的场地。		
15			文化活动中心	4 组	80 ㎡ / 个	19.2	省定贫困村资金	2018 年	2018-2019 年	各自然村结合自身设施配套情况设置		
16			篮球场	1 组、8 组	2 个	44	省定贫困村资金	2018 年	2018-2019 年	各自然村结合自身设施配套情况设置		
17			健身室	结合村委设置	45 ㎡	5	省定贫困村资金	2018 年	2018-2019 年	结合村委设置		
18			图书室	结合村委设置	50 ㎡	——	省定贫困村资金	2018 年	2018-2019 年	结合村委设置		
19		公共场地	健身活动场所	13 组	1 套	0.2	省定贫困村资金	2018 年	2018-2019 年	现状已硬底化，规划增设建设器材		
				1 组、2 组、9 组	2483 ㎡	111.7	省定贫困村资金	2018 年	2018-2019 年	硬底化铺装、添加绿化、休闲桌椅等；另外增加增加如乒乓球桌、揉推器、扭腰器等健身设施；可兼作停车场。		
			休闲活动场所	新村、9 组、13 组	905 ㎡	27.4	省定贫困村资金	2018 年	2018-2019 年	结合绿地，打造为设有防护栏杆、凉亭、绿化、景观小品等设施，供村民日常游憩的公共绿地。		
总计						1504.6	备注：其中资金筹措方式为省定贫困村的资金为 1299.3 万元					

7.土地利用汇总表


用地代码	用地名称		用地面积（hm ² ）		占总用地范围面积的比例（%）		人均村庄建设用地面积（m2/ 人）	
			现状	规划	现状	规划	现状	规划
V	村庄建设用地		30.75	32.77	7.54	8.04	150	149.98
	其中	V1 居住用地	28.12	28.12	6.9	6.9	137.17	128.7
		V2 村庄公共服务用地	0.68	2.32	0.17	0.57	3.32	10.62
		V3 村庄产业用地	0	0	0	0	0	0
		V4 村庄基础设施用地	1.95	2.33	0.48	0.57	9.51	10.66
N	非村庄建设用地		14.98	14.98	3.67	3.67	-	-
	其中	N1 对外交通设施用地	1.1	1.1	0.27	0.27	-	-
		N2 国有建设用地	13.88	13.88	3.4	3.4		
E	非建设用地		362.02	360	88.78	88.29	-	-
	其中	E1 水域	20.95	20.95	5.14	5.14	-	-
		E2 农林用地	341.07	339.05	83.65	83.15	-	-
总用地范围			407.75	407.75	100	100	-	-
备注：2016 年常住人口 2050 人（其中：户籍人口 2663 人）								
依据过去五年平均增长率 0.71%，预测 2025 年常住人口 2185 人。								

(二) 云浮市新兴县河头镇料坑村社会主义新农村示范村整治创建规划

1.村庄现状情况图

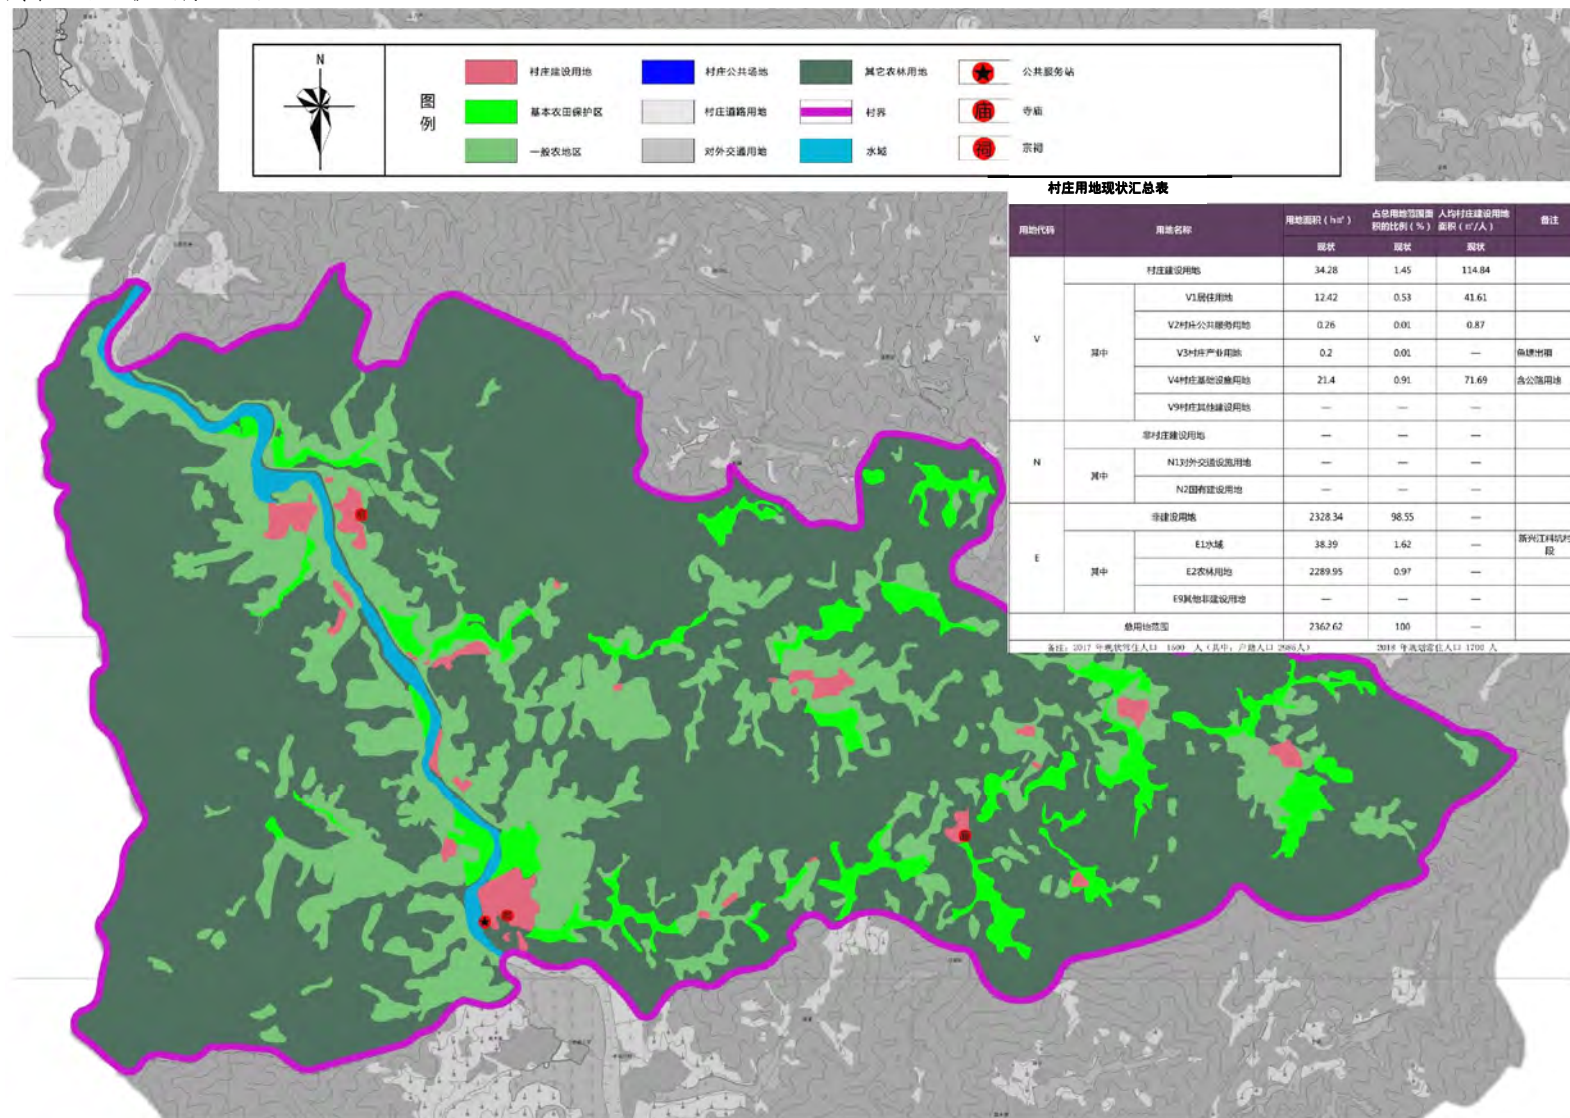

2.村庄用地布局规划图

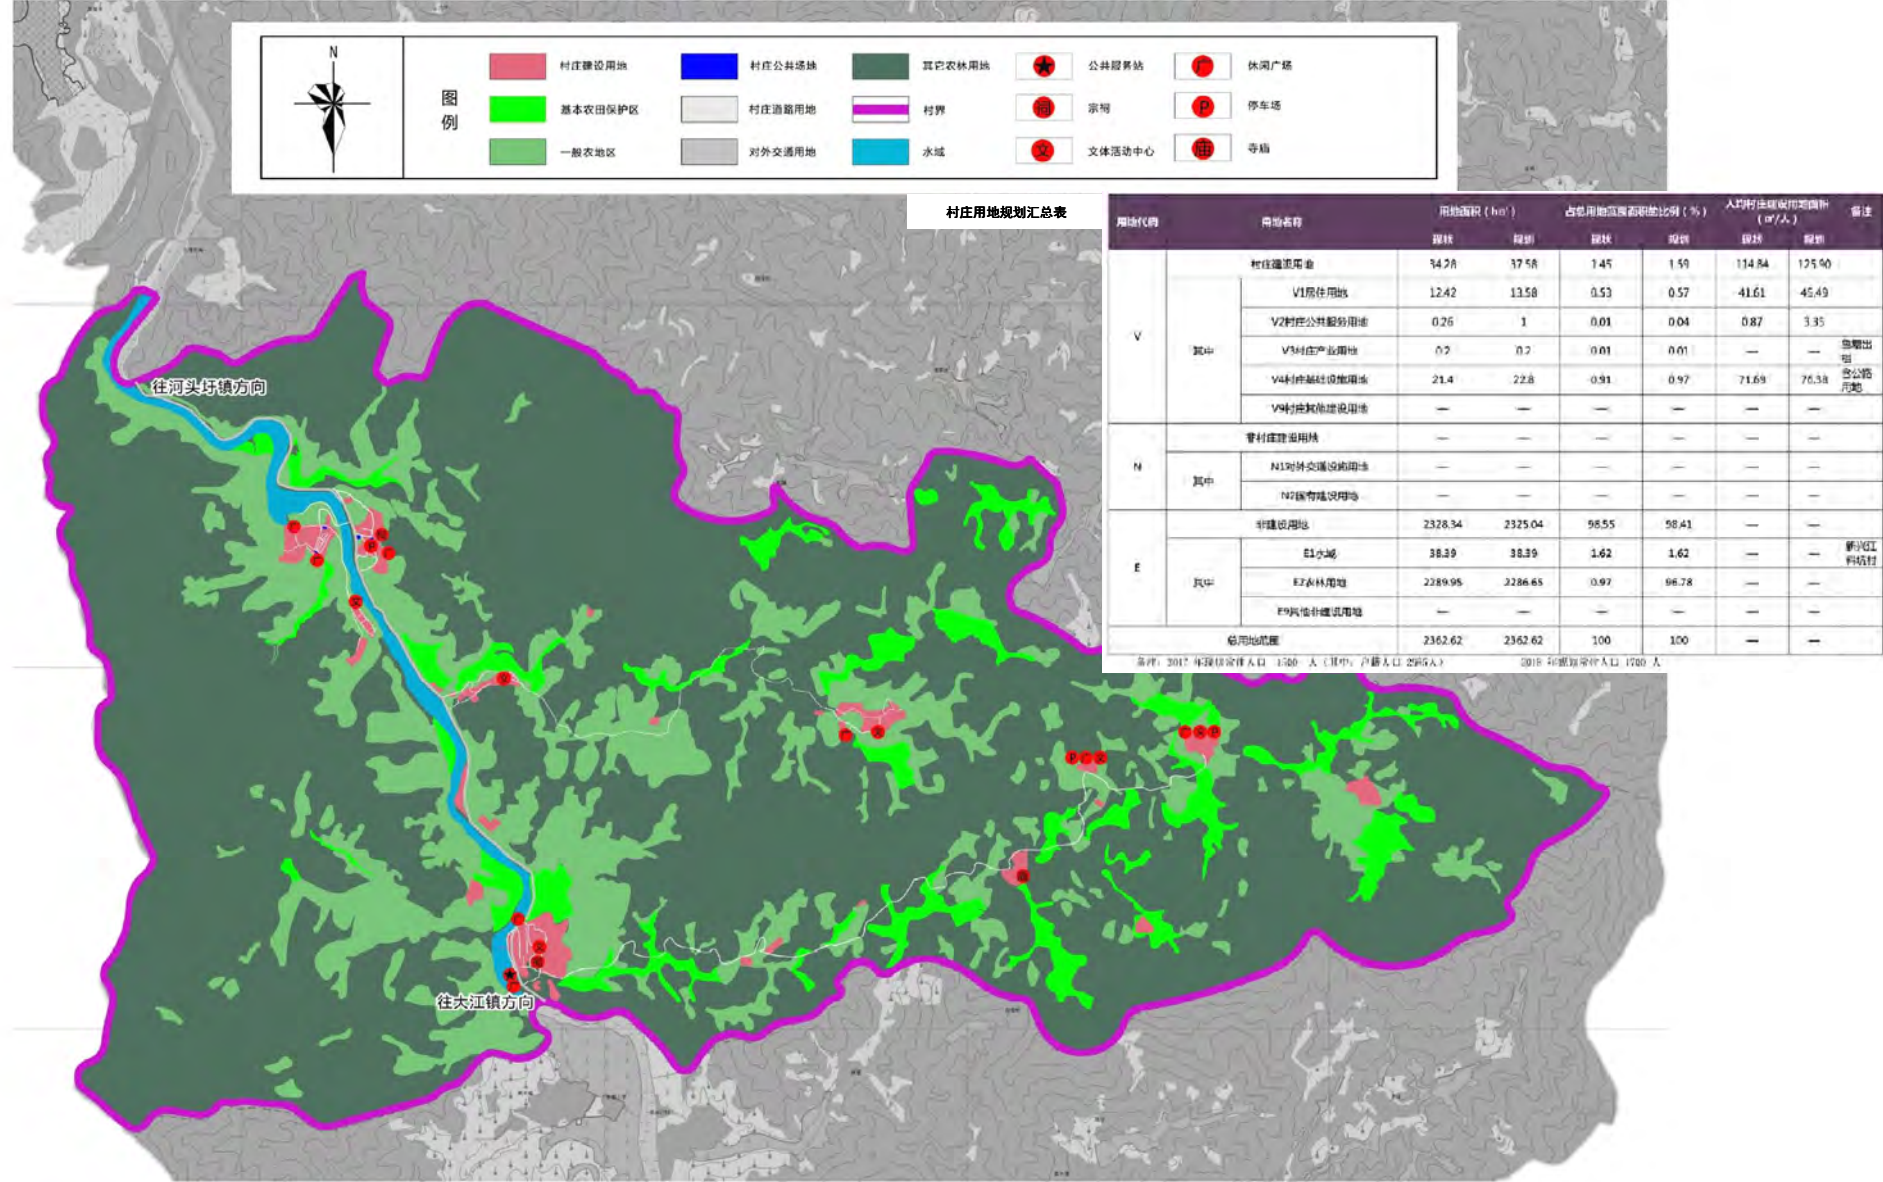


3.村庄规划建设项目布局图




- 1 道路
- 2 休闲公园
- 3 停车场
- 4 文化楼
- 5 卫生间
- 6 垃圾收集点
- 7 护坡
- 8 饭堂修缮
- 9 污水处理池
- 10 庙
- 11 新建球场
- 12 护栏
- 13 集中供水水源
- 14 文化楼
- 15 球场
- 16 小广场
- 17 旧队址修缮
- 18 小公园



4. 农房建设规划平面图

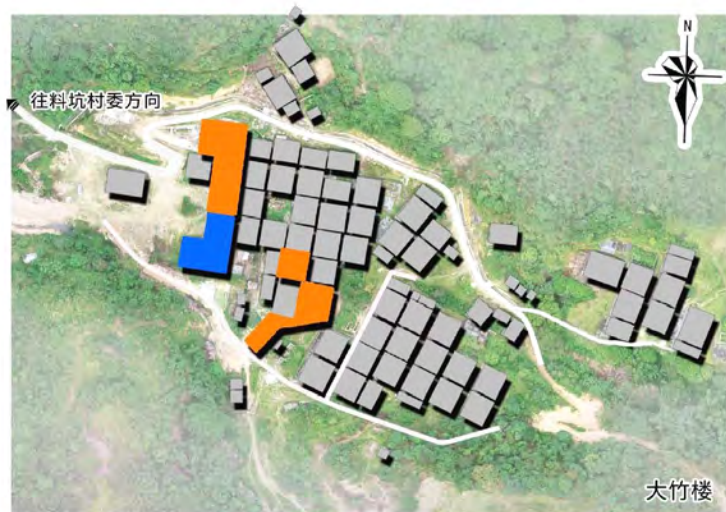

- 保留房屋
- 整治房屋
- 拆除房屋

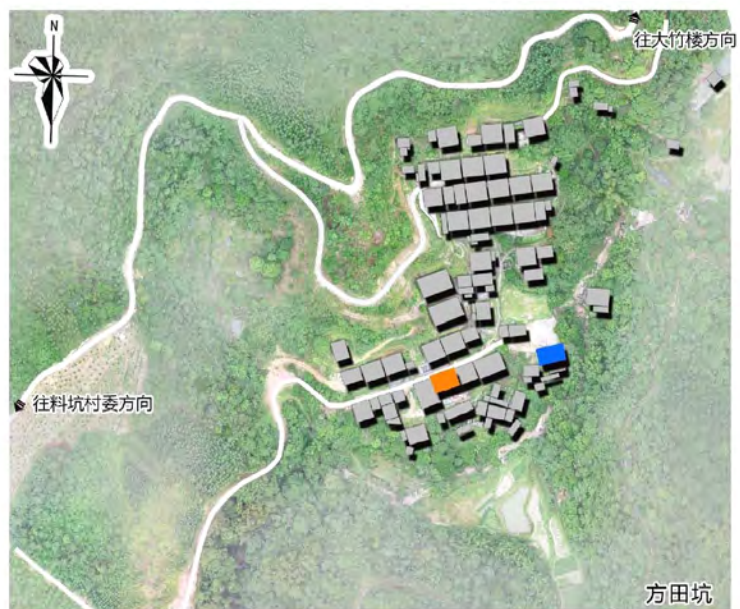

5.村庄规划建设管理公约

第一条：为加强料坑村规划建设管理，根据有关管理规定，结合本村实际情况，特制订本公约，全体村民必须遵守。

第二条：本村成立村民小组，负责监督管理村中公共事务和收集并向村委反映村民对村庄建设的建议、意见。

第三条：任何单位和个人不得擅自道路两侧、公共场地设置广告招牌、张贴栏等物。因实际情况需要设置的，必须向村委会提出申请，经村委会主管领导批准，并交纳押金，申请期限到后必须自行安全拆除或向村委会提出续期申请，经批准后方可继续设置。设置的广告牌必须内容规范健康，构图色调美观。

第四条：保护村内所有公共设施和绿化设施，人人有责。任何人未经允许，不得毁坏村庄内公用桌椅、健身设施、垃圾桶、路灯等，不得砍伐树木、采摘花草，不得在公用设施附近堆放杂物、垃圾等。任何组织或个人不得破坏、侵占公共绿地。

第五条：禁止在建筑物及树木上涂写、刻画或张贴各类广告和宣传品。禁止乱丢果皮、纸屑、烟蒂、杂物，禁止从高处泼水、抛垃圾和杂物。禁止将垃圾直接倒入污水管道、池塘、河流。

第六条：本村设立垃圾收集点和垃圾收集站，村民不得随意移动，阻挠建设，本村聘请卫生保洁员，负责村内公共区域的清扫和保洁，并清理每天垃圾收集点垃圾，转运到垃圾收集站分类处理。

第七条：住户门前实行“三包”，对在房前屋后乱吐、乱丢、乱贴、乱摆等违章行为要进行监督。住户投放垃圾要确保垃圾入桶，要杜绝把垃圾堆放到垃圾桶四周的行为。提倡垃圾袋装化，提倡垃圾分类，鼓励住户回收可利用的垃圾。

第八条：施工场地的垃圾由施工单位负责清扫保洁及垃圾收运，由建设项目主管单位负责施工环境管理，严格遵守建筑工地施工现场管理规定以及建筑垃圾和工程渣土处置管理规定。

第九条：鼓励村民主动参与村庄环境整治项目行动，落实“三清理、三拆除、三整治”，主动参与村巷道及生产工具、建筑材料乱堆乱放的清理、房前屋后和村巷道杂草杂物、积存垃圾的清理、沟渠池塘溪河淤泥、漂浮物和障碍物的清理；主动参与村中危旧房、废弃猪牛栏及露天厕所茅房、乱搭乱建、违章建筑、非法违规商业广告、招牌等的拆除工作；主动参与整治村中生活垃圾、生活污水等工作。

第十条：爱护村中供水、排水设施，村内实行雨污分流统一规划，村民不得私自接驳，乱排放生活污水。房屋排水借口需向村民小组确认后在进行建设。

第十一条：村中电力、电信线路需按规划统一接驳、严禁村民私自乱拉乱接，影响村容村貌。

第十二条：农村宅基地应统一集中安排，整体规划。村民自建房需符合

村庄房屋建设规划，不准未批先建和违章搭建。新建房屋建筑风格应参照本次规划的样式进行，并统一建筑坐向、高度、间距、外立面样式，建筑之间应留有足够的人行通道，使村庄农房建筑风貌更规整。

第十三条：村民需保护村内祠堂、寺庙、古老大屋等具有传统岭南古建筑特征的历史文化建筑、古树名木和水井，村民不得私自连接用水管到水井。

第十四条：建设过程中需要占用公共用地的，需经村民小组的批准同意，并应保持村内道路的畅通和环境清洁，合理安排作业时间，做到文明施工，避免对村民生活造成滋扰。

第十五条：村民相互监督，如有对抗整治行动、侵占破坏公共设施、违规建房等行为，由村民小组进行批评教育、责令改正，屡教不改的，在村务公开栏曝光。情节严重的，由村民小组上报村委会作严肃处理；触犯法律需追究责任的，交由司法机关处理。

第十六条：本公约经村民代表大会 2017 年 12 月 17 日讨论通过，自公布之日起实施。


新兴县河头镇料坑村民委员会（章）

2017 年 12 月 17 日


省定贫困村创建社会主义新农村示范村 料坑村 PAGE

(三) 汕头市潮南区井都镇平湖东村社会主义新农村示范村整治创建规划

1.村庄现状情况图

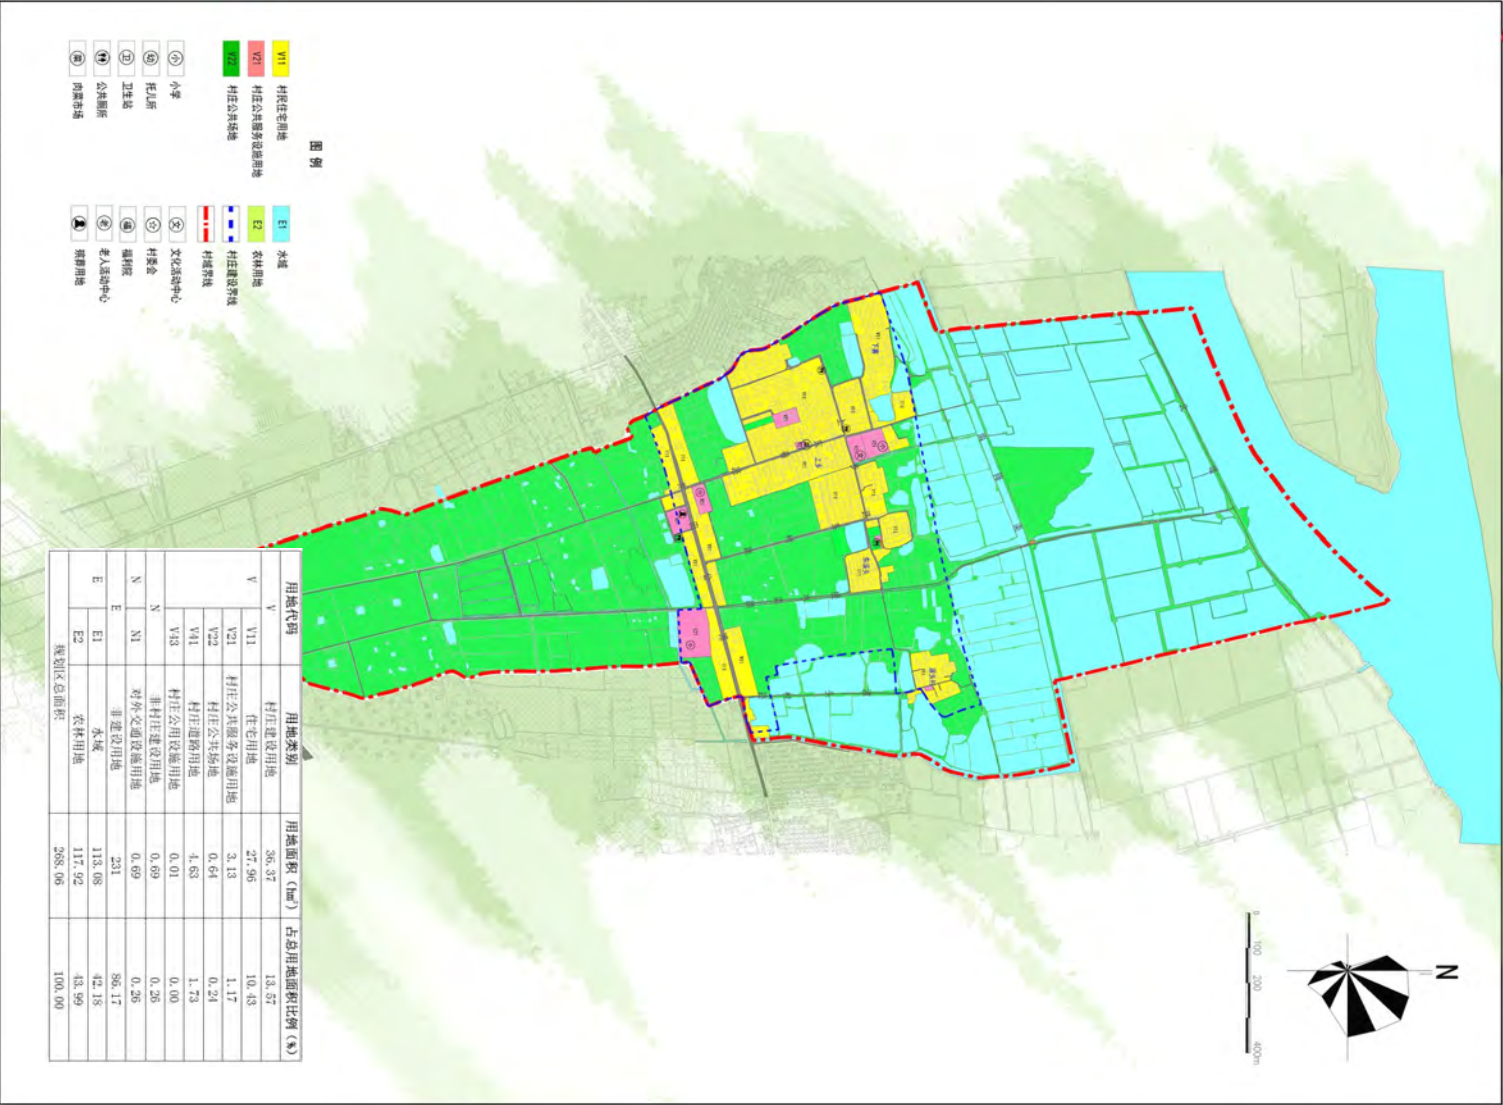

2.村庄用地布局规划图

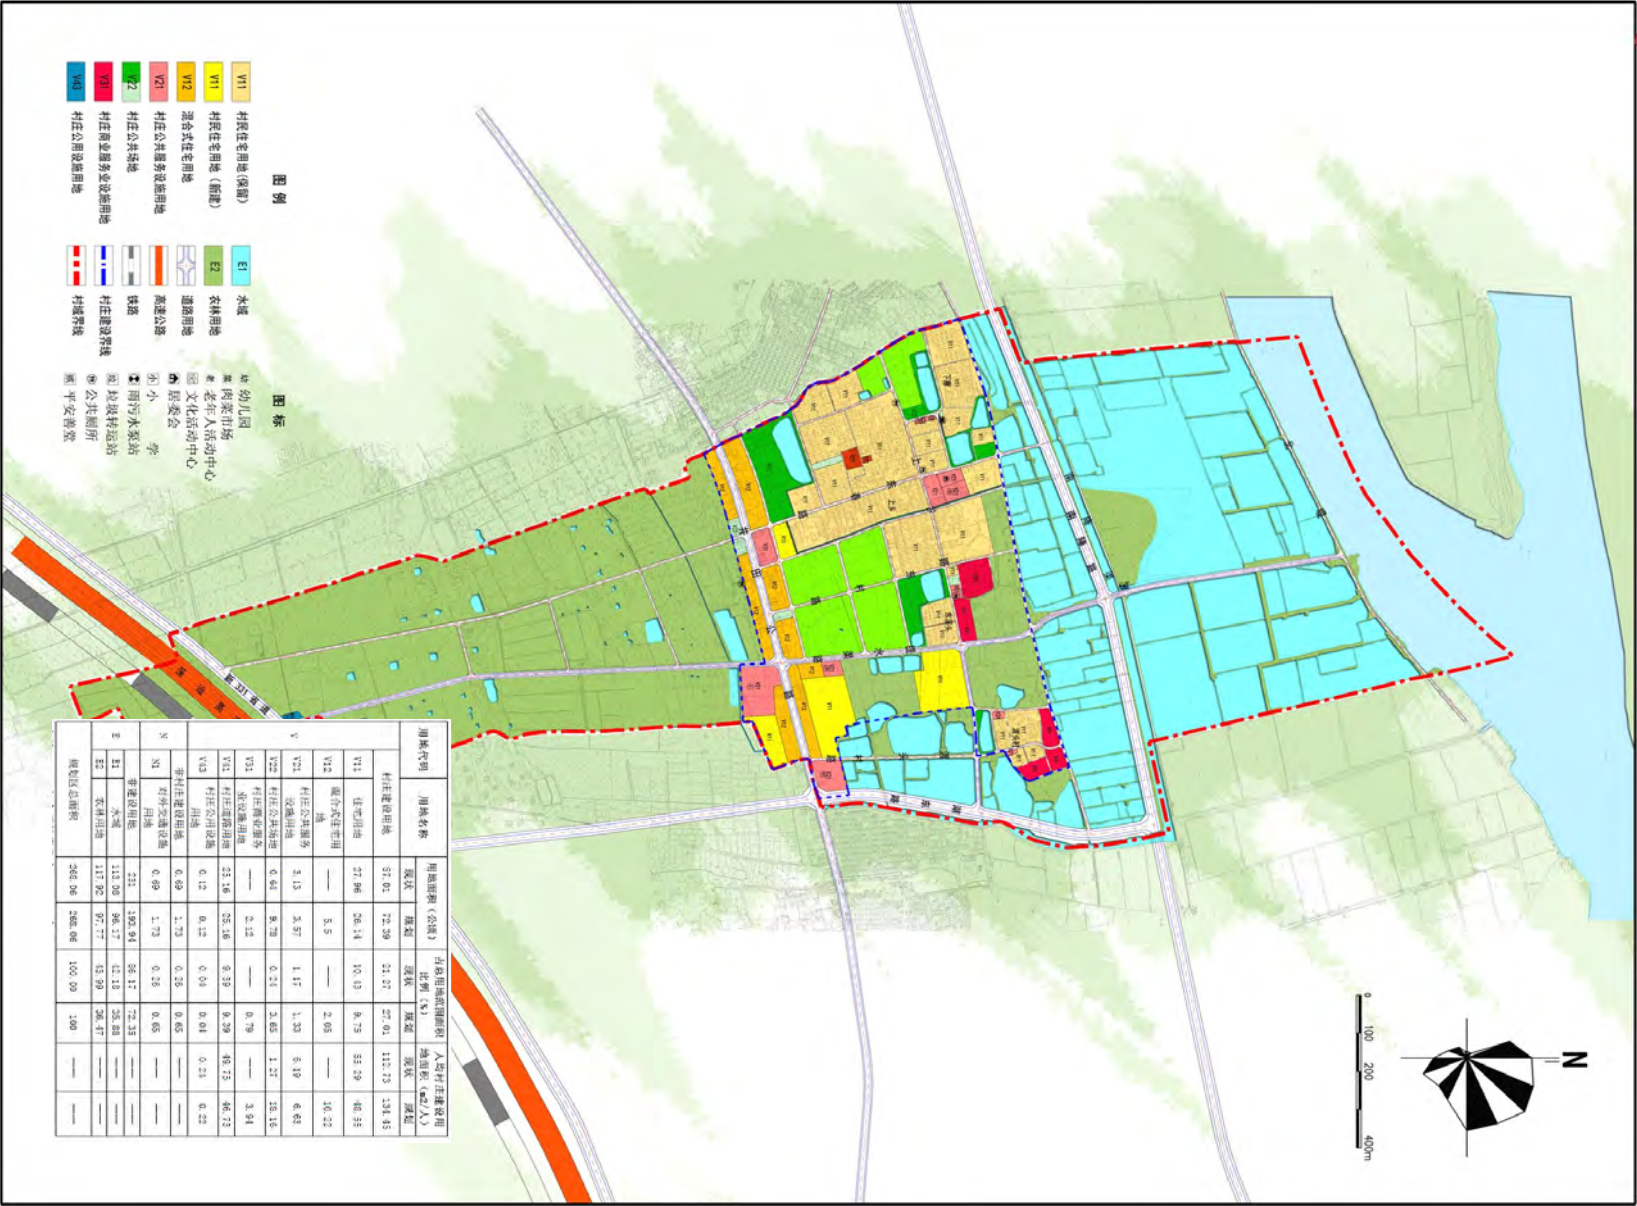


3.村庄规划建设项目布局图



项目类型	序号	项目名称
村庄风貌整治	1	村入口牌坊建设
	2	村标识牌、指示牌建设
	3	主要道路沿线立面整治
	4	村内风水池环境提升
	5	对村庄进行“三清三拆”
	6	戏台改造
垃圾处理	7	宣传栏
	8	垃圾箱
	9	垃圾收集车
	10	垃圾转运站
	11	公厕
污水处理	12	村内小型截洪沟、排水沟渠清淤
	13	渡头渠改造
	14	上乡排水渠改造
	15	生态污水处理池
	16	排水泵站建设
	17	渡头自然村
	18	一套污水处理系统
	19	东溪头自然村
	20	上乡自然村
	21	下寨自然村
	22	渡头村路
村道硬化	23	上乡路东延至渡头段
	24	环堰路
	25	机耕路
	26	村支路硬化
	27	渡头自然村
	28	东溪头自然村
	29	村内巷道硬化
	30	上乡自然村
	31	下寨自然村
	32	全村监控系统
	33	道路亮化、绿化工程
设施完善	34	文化活动广场
	35	医疗站
	36	文化站
	37	肉菜市场改造提升
	38	福利社
	39	便民服务中心
	40	自来水管网升级
	41	敬老院
	42	老人活动中心
	43	新村公共配套中心

4.村庄建筑改造提升方案图

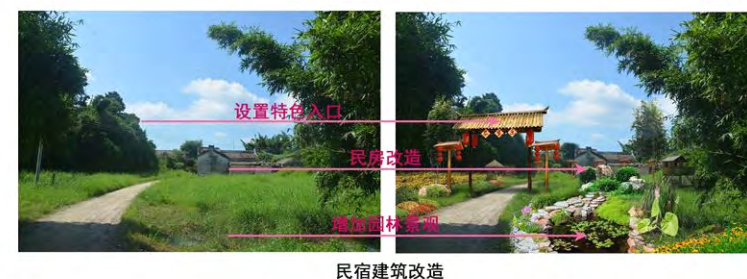



规划新建建筑布局图



新建一户一宅



新建农民公寓

规划新建建筑意向



道路环境整治意向




村入口景观整治




文化活动的站意向

（四）珠海市斗门区莲江村名村建设规划

1.村庄现状情况图

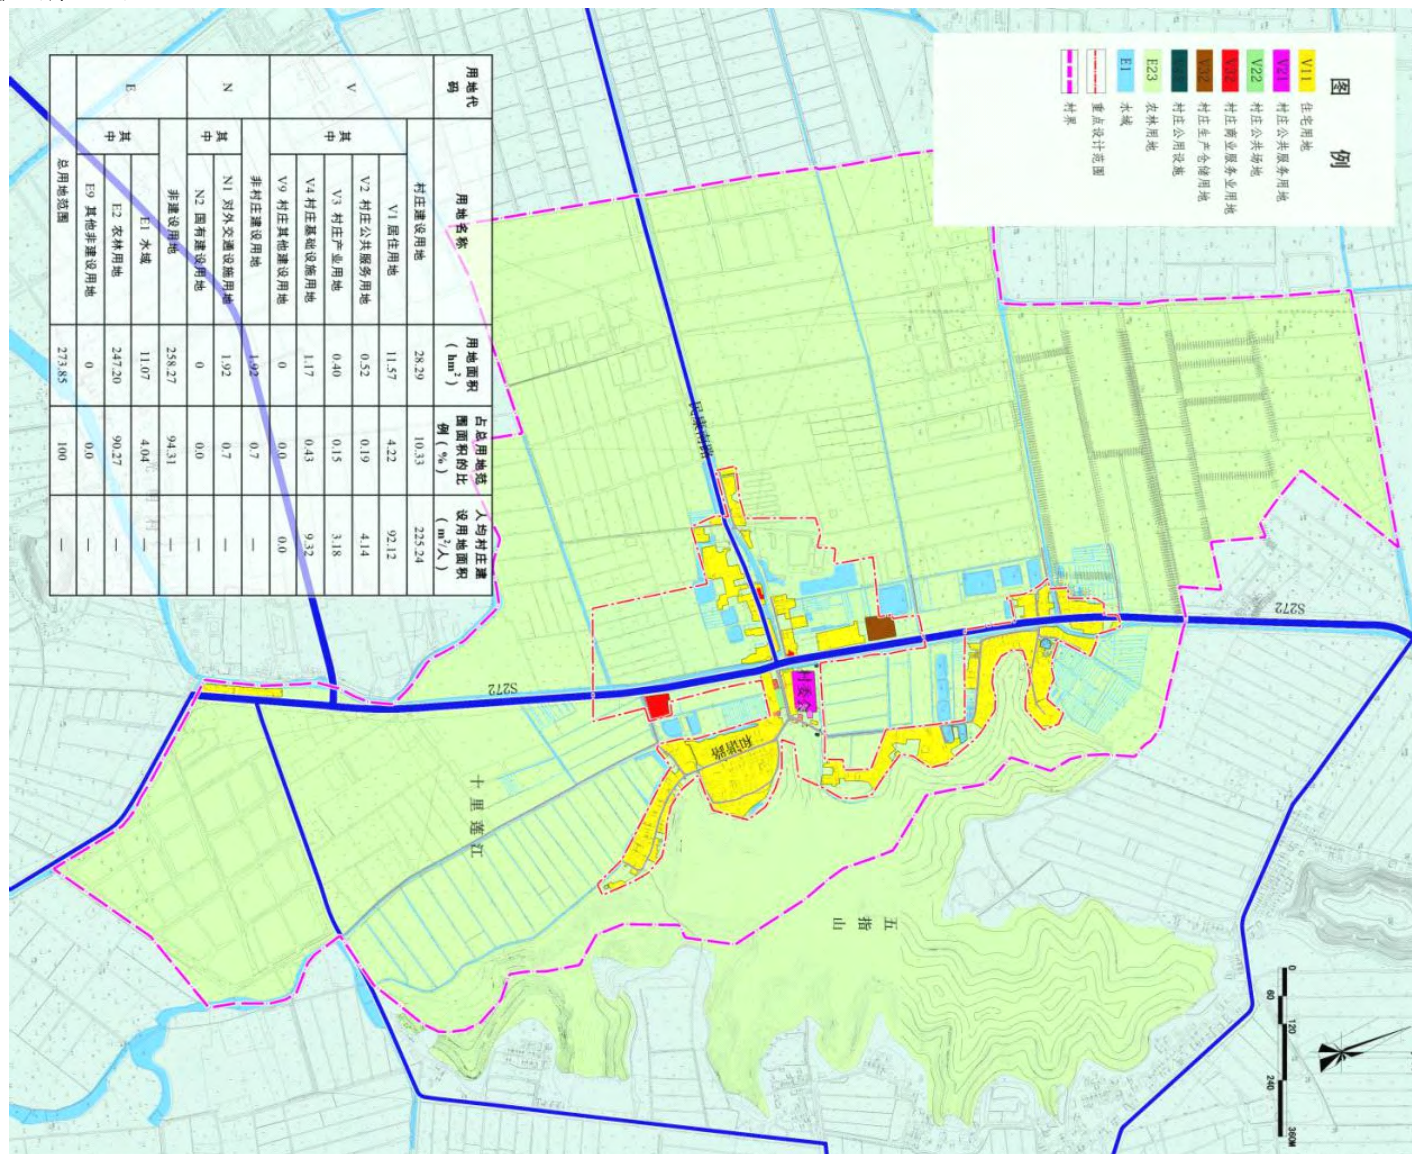

2.村庄用地布局规划图

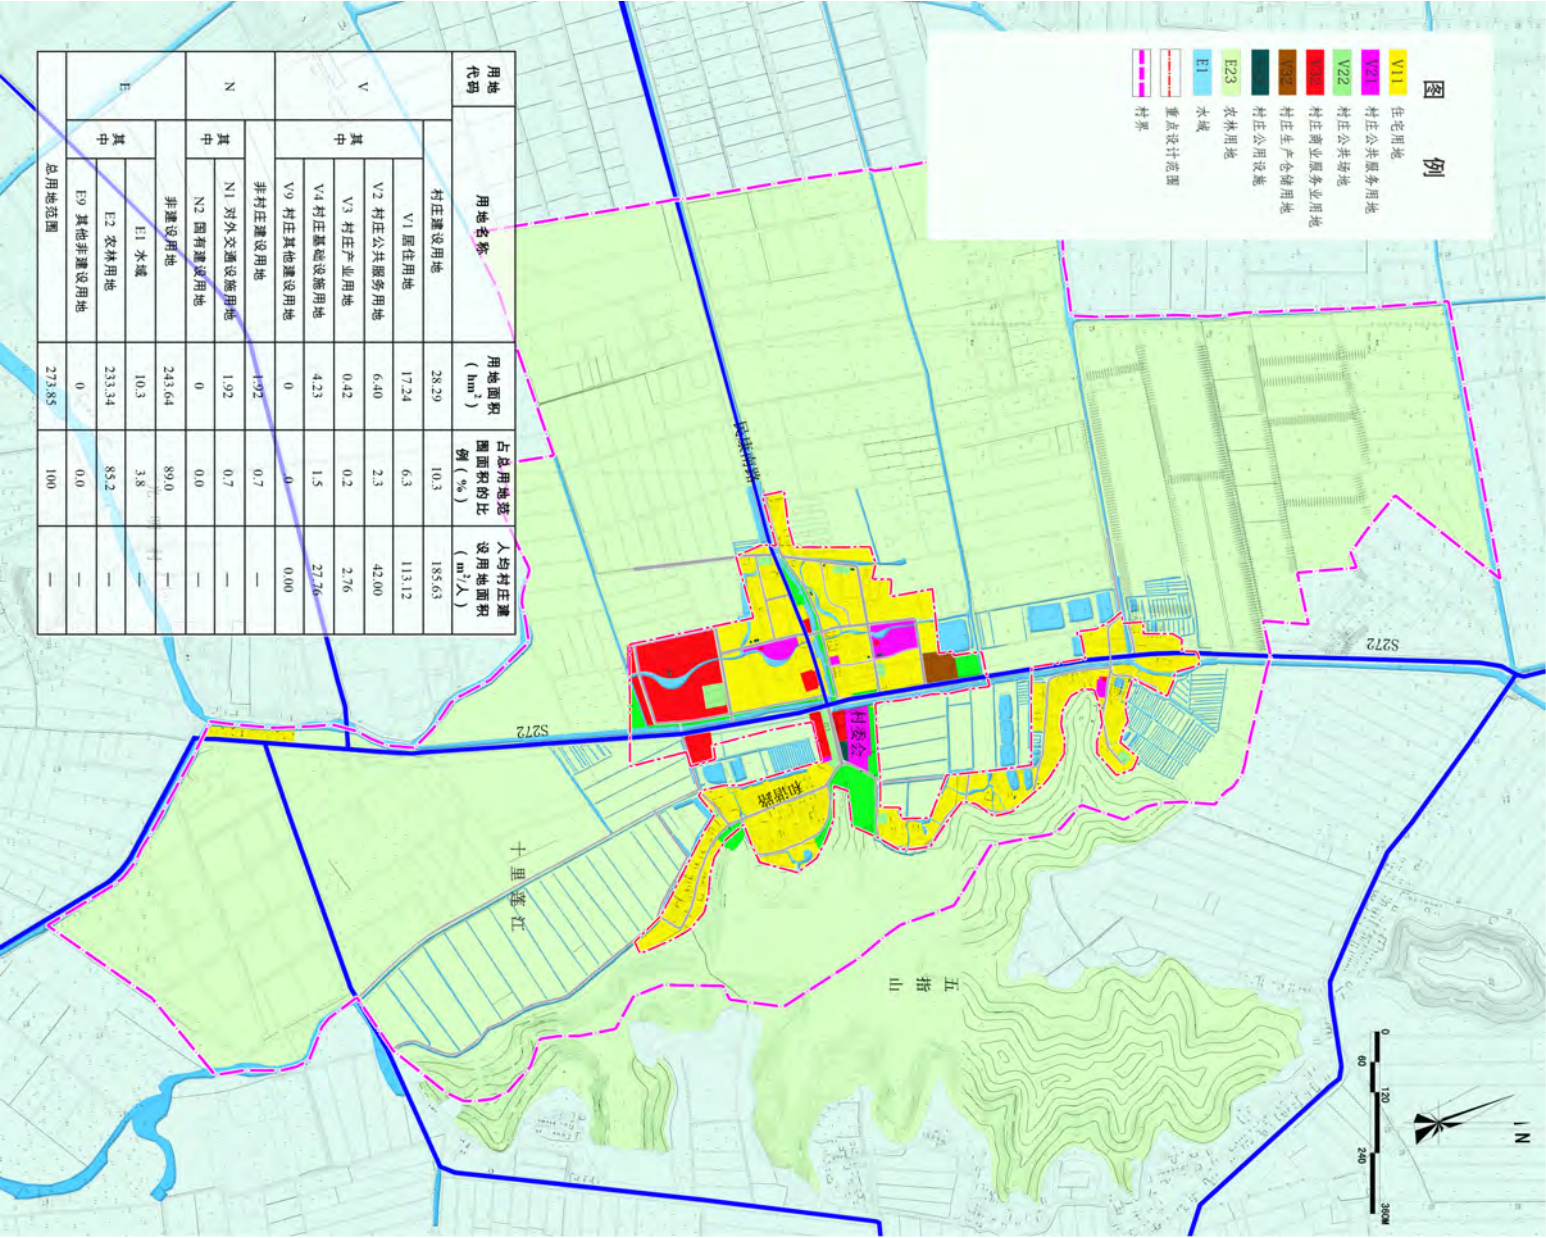

3.村庄规划建设项目布局图



4.村庄建筑改造提升方案图



编制人员名单

主编单位：广东省住房和城乡建设厅

主 编：赵 坤、张少康

副 主 编：刘 玮

顾 问：蔡 瀛、魏振发

技术审核：李永洁

参加人员：宋 健、王 务、苏智云、李宏林、杨 丽

承编单位：华南理工大学广东省村镇可持续发展研究中心

参加人员：叶 红、李贝宁、陈 可、卫敏辉、

孔祥莹、陈烙文