


清远市清城区2020年度第五十九批次(地块一)城镇建设用地平面图

清远市测绘地理信息中心

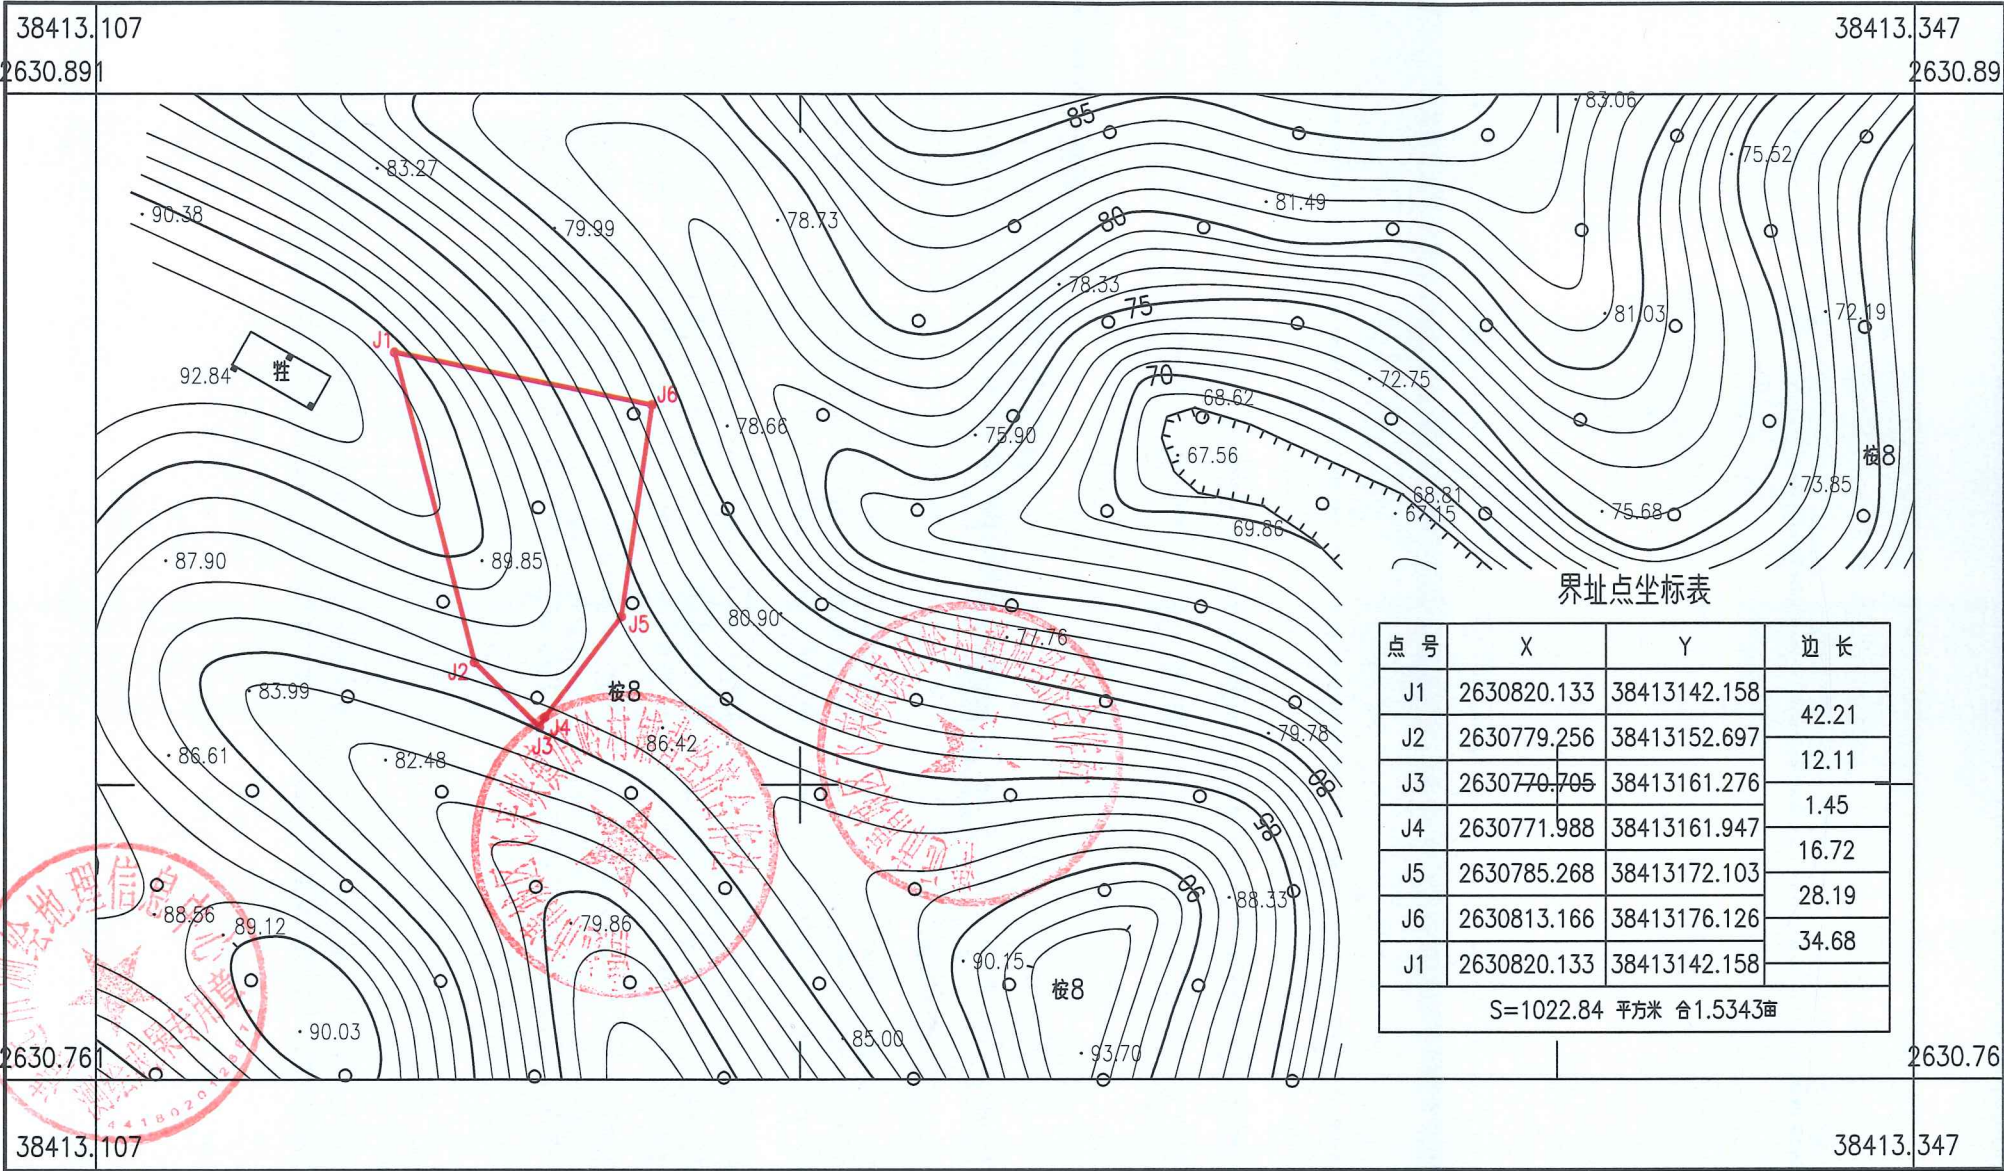


2020年11月数字化成图
2000国家大地坐标系
1985国家高程基准
2017年版图式

1:1000

测量员：周中莹
绘图员：龙 聪
检查员：孔 明

清远市清城区2020年度第五十九批次(地块二)城镇建设用地平面图

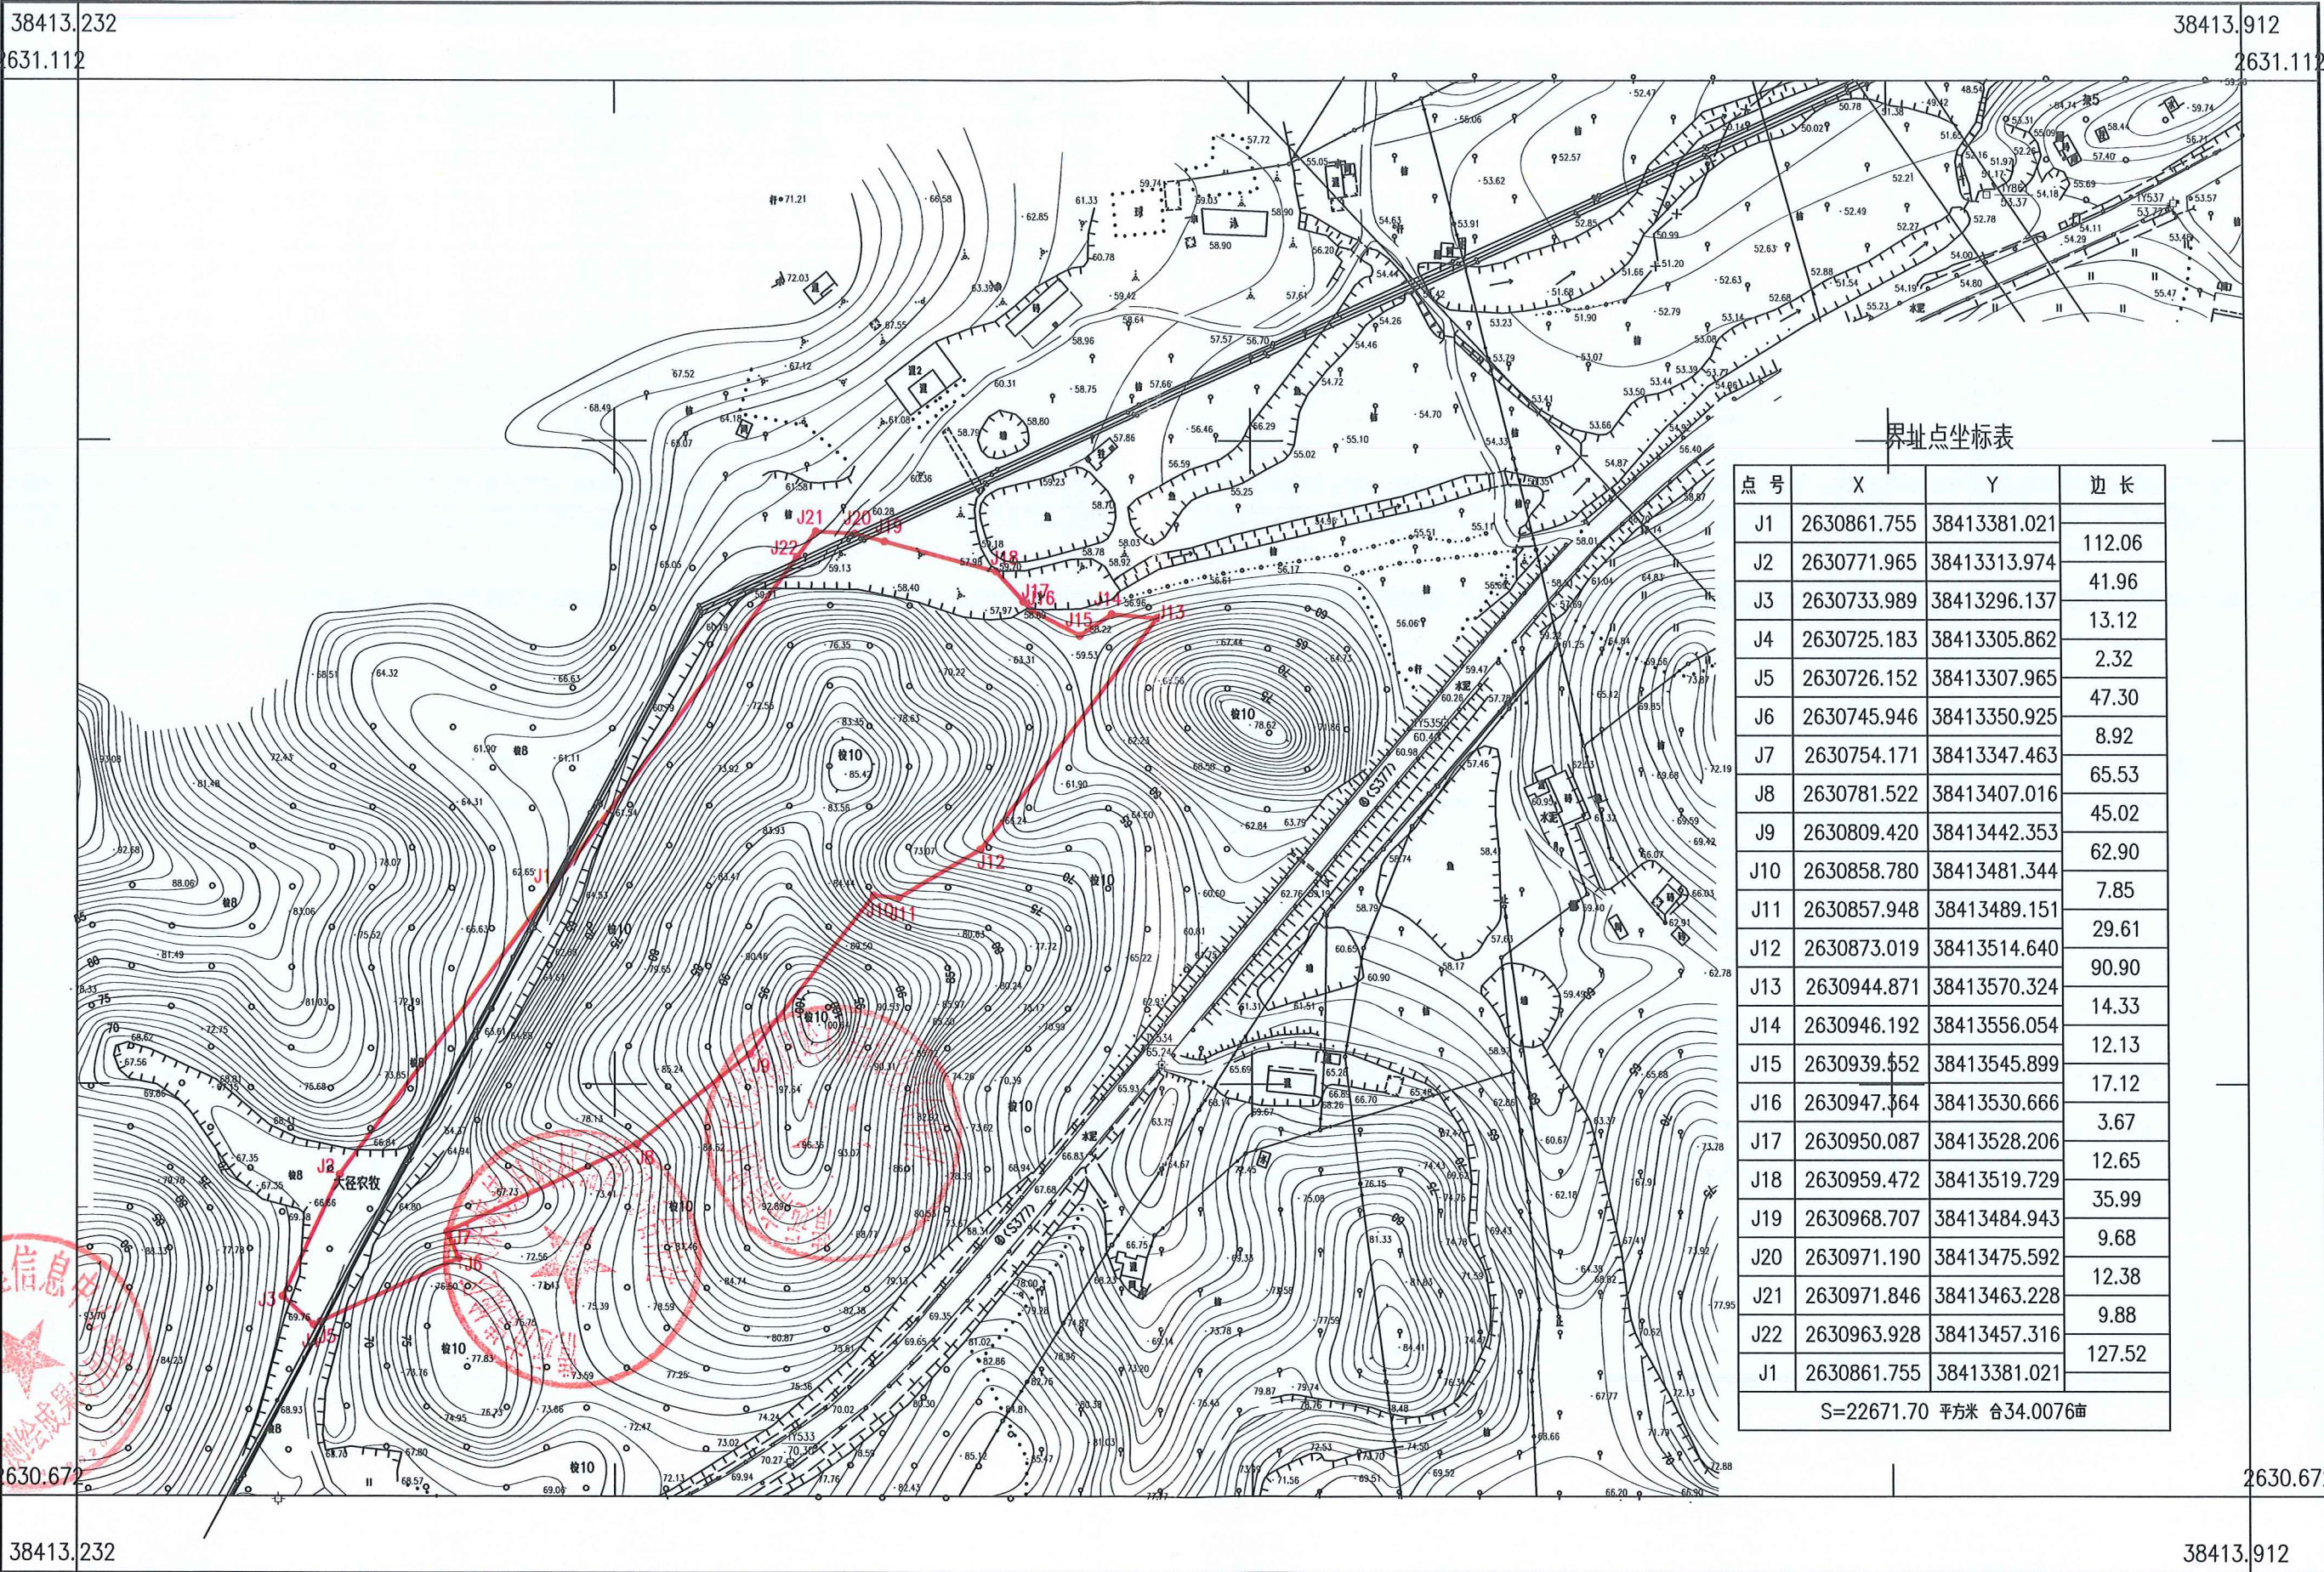

界址点坐标表

点号	X	Y	边长
J1	2630861.755	38413381.021	112.06
J2	2630771.965	38413313.974	
J3	2630733.989	38413296.137	41.96
J4	2630725.183	38413305.862	13.12
J5	2630726.152	38413307.965	2.32
J6	2630745.946	38413350.925	47.30
J7	2630754.171	38413347.463	8.92
J8	2630781.522	38413407.016	65.53
J9	2630809.420	38413442.353	45.02
J10	2630858.780	38413481.344	62.90
J11	2630857.948	38413489.151	7.85
J12	2630873.019	38413514.640	29.61
J13	2630944.871	38413570.324	90.90
J14	2630946.192	38413556.054	14.33
J15	2630939.552	38413545.899	12.13
J16	2630947.564	38413530.666	17.12
J17	2630950.087	38413528.206	3.67
J18	2630959.472	38413519.729	12.65
J19	2630968.707	38413484.943	35.99
J20	2630971.190	38413475.592	9.68
J21	2630971.846	38413463.228	12.38
J22	2630963.928	38413457.316	9.88
J1	2630861.755	38413381.021	127.52
S=22671.70 平方米 合34.0076亩			

清远市测绘地理信息中心

2020年11月数字化成图
2000国家大地坐标系
1985国家高程基准
2017年版图式

1:2000

测量员: 周中莹
绘图员: 龙 聪
检查员: 孔 明